

SMART BUILDING URUGUAY

Locales comerciales Avda. Pedragosa Sierra

Padrón 10596 · Punta del Este, Maldonado

Material de base para el proyecto ejecutivo y el permiso de construcción
Para: Arq. Pablo Alcoba · 12 de noviembre de 2026

Programa	4 locales comerciales en cáscara + baño, planta de 25 × 10 m (250 m²), sin columnas interiores
Estructura	Pórticos metálicos cada 5 m, platea H30 con vigas de fundación (cálculo: Ing. Ricardo Portugau)
Envolvente	Muros de panel EPS, techo de panel PIR, vidriera continua a la plaza, faja, brise de madera y cenefa negra
Obra	SBU · Ramiro Portugau, director de obra


Láminas

1. Implantación: planta completa con el terreno
2. Planta de arquitectura
3. Sanitaria: planta general
4. Sanitaria: local tipo
5. Eléctrica: planta general
6. Eléctrica: local tipo
7. Fachada norte (a la plaza)
8. Fachada este (a la avenida) y corte
9. Detalle del frente: cenefa, brise símil madera y faja
10. Render del anteproyecto (del cliente)

Implantación: planta completa con el terreno

Implantación · padrón 10596

escala gráfica: 1 m = 22 px · FOS 25 % · 6 estacionamientos (pide 3)

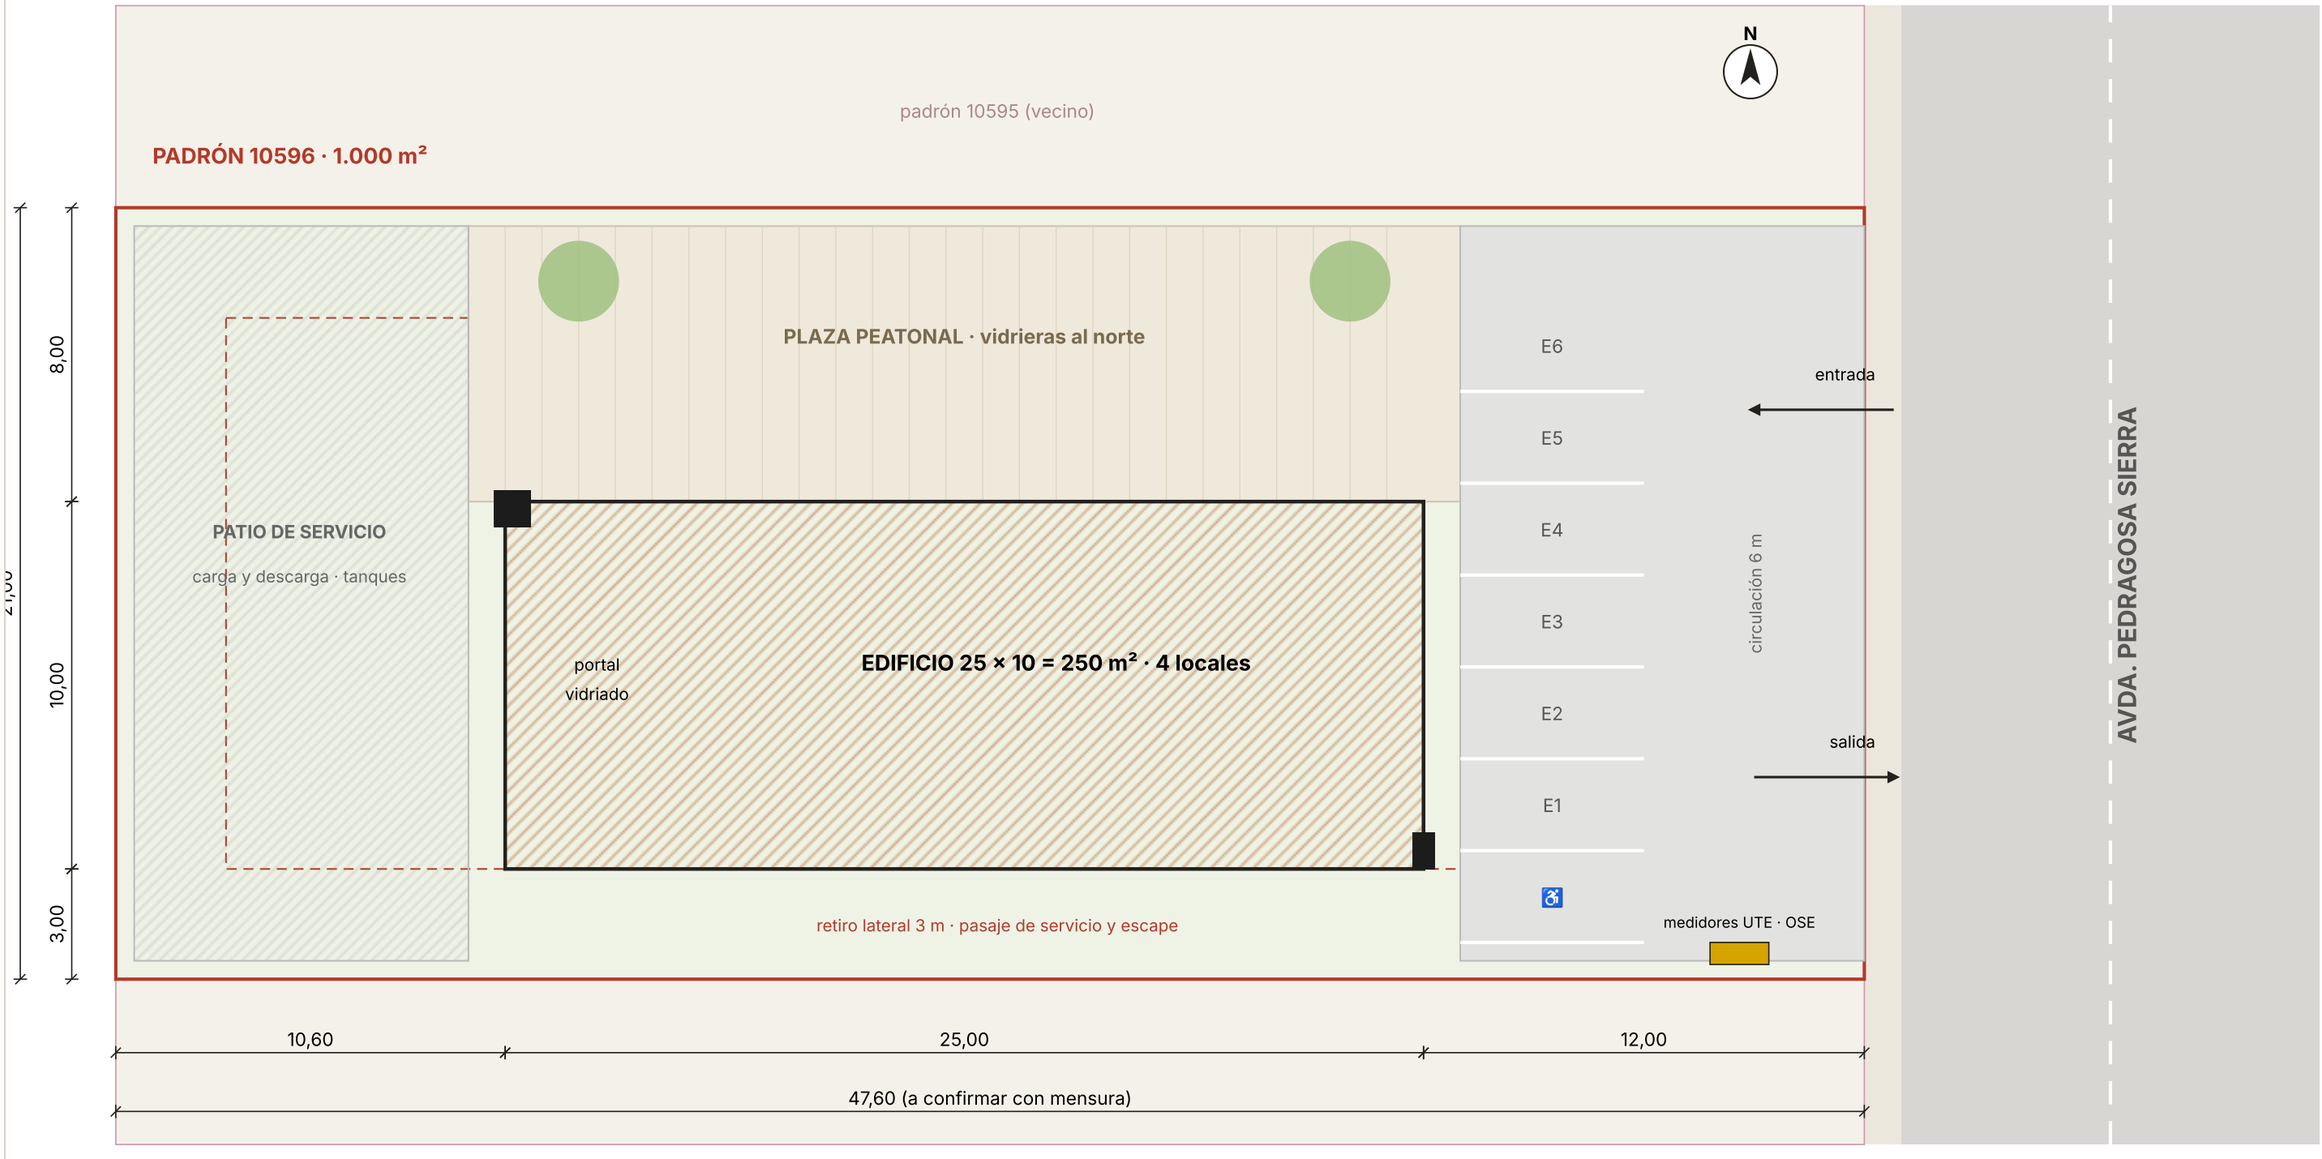


Planta de arquitectura

Locales comerciales · Avda. Pedragosa Sierra · Padrón 10596
Para Arq. Pablo Alcoba · 12 de noviembre de 2026 · lámina 2/10

Planta · 4 locales


ejes cada 5 m · luz libre 10 m · cotas parciales y acumuladas desde el eje 1

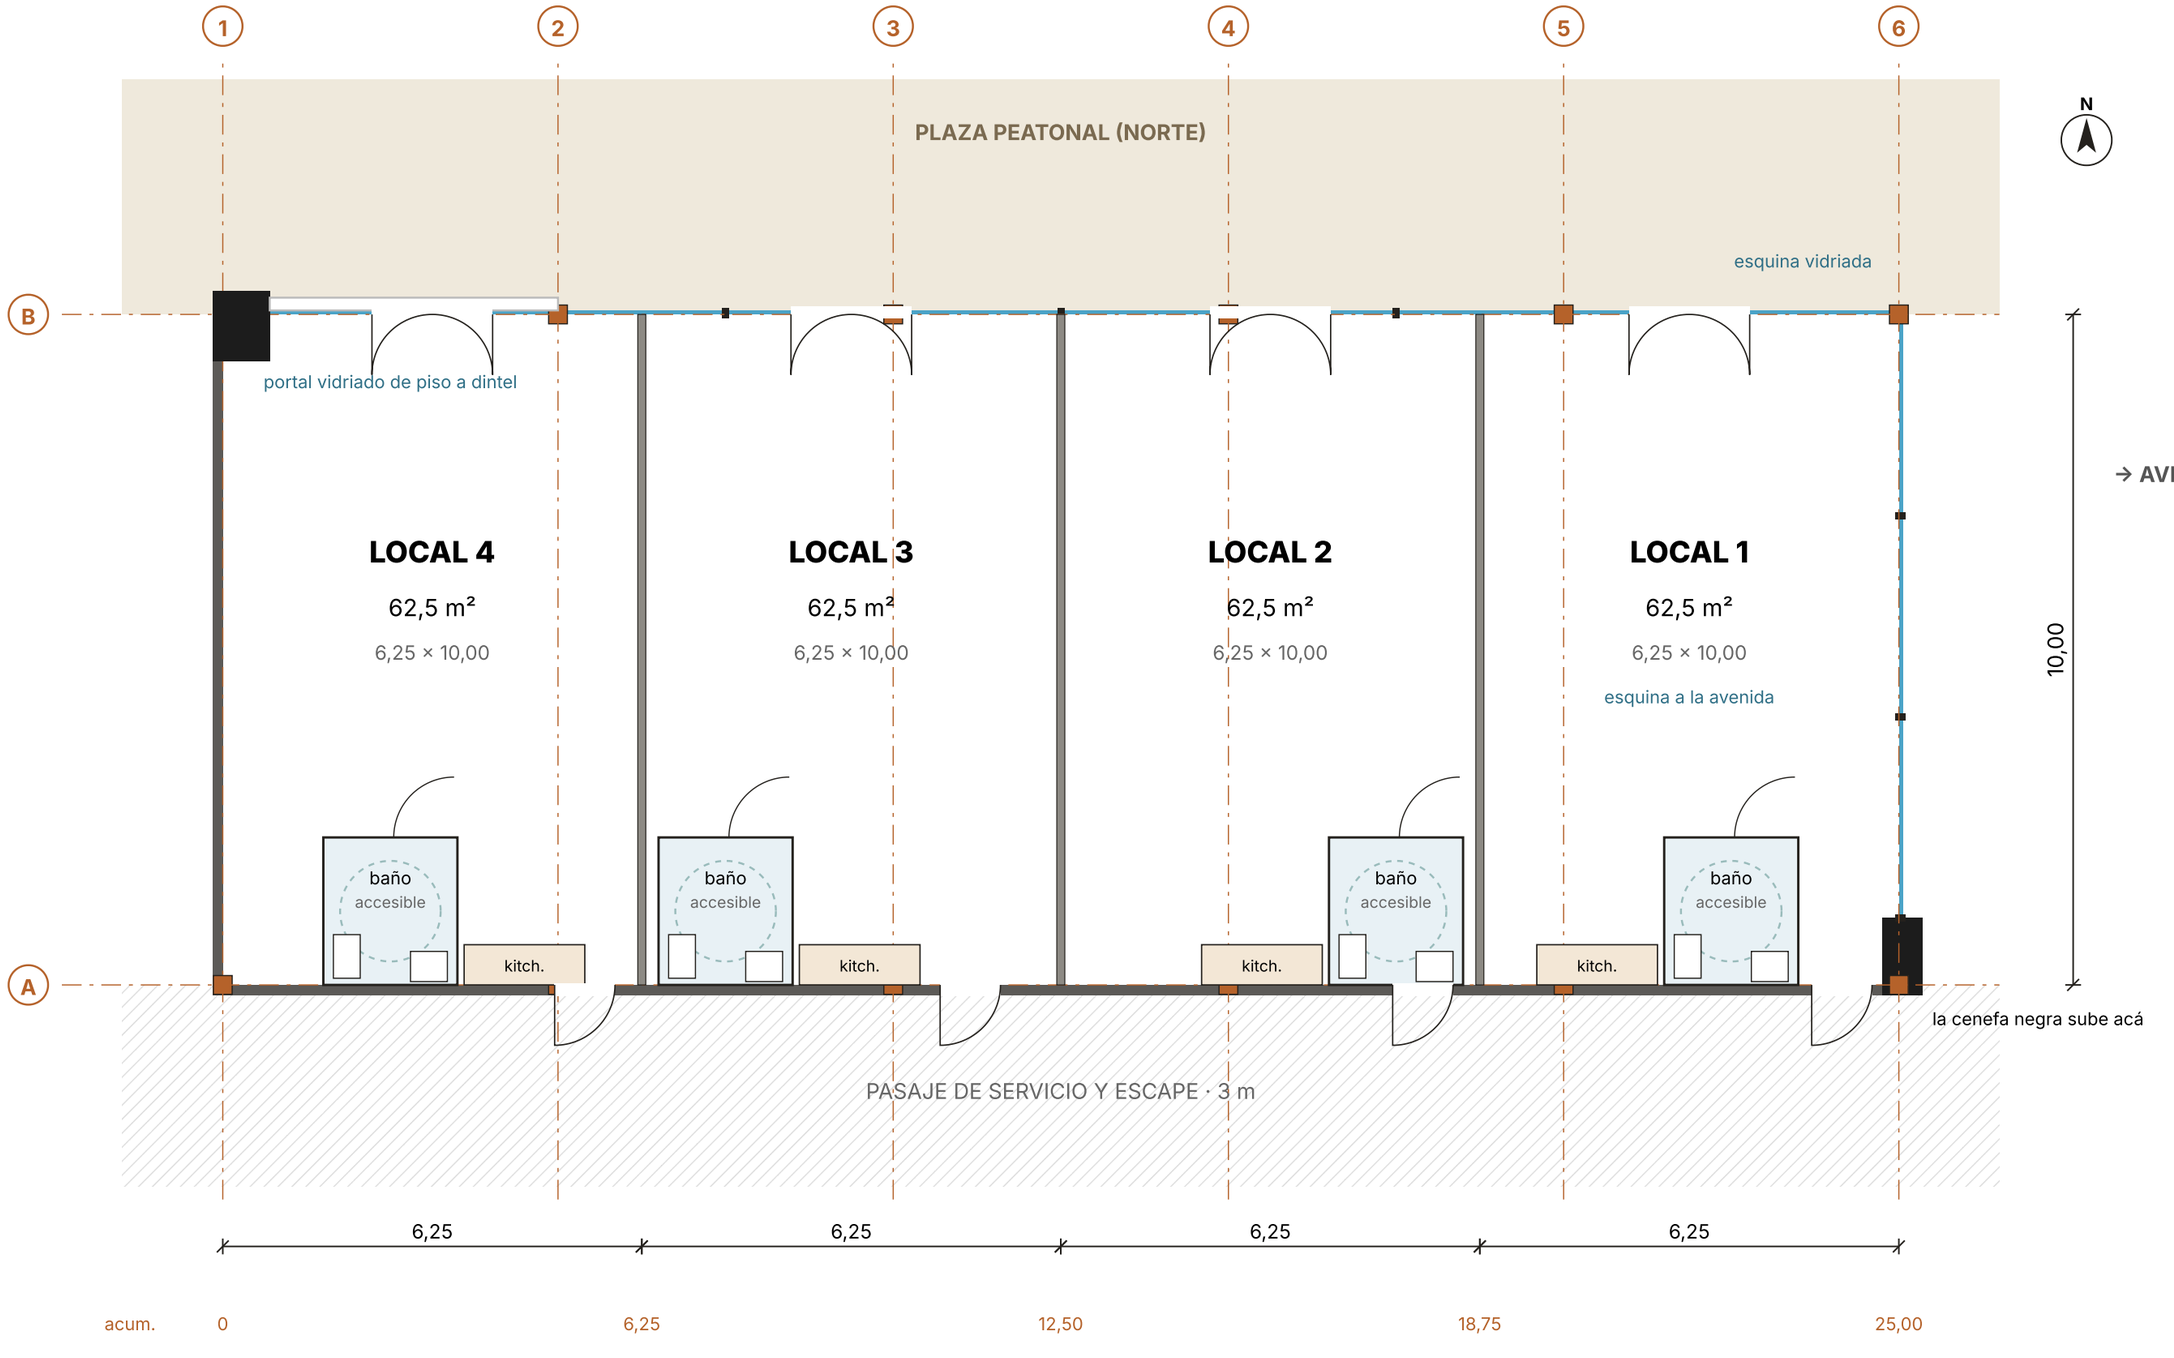

Sanitaria: planta general

Sanitaria · planta general · 4 locales base

desagües bajo platea y por el pasaje, pluviales a cuneta, agua con batería de submedidores en el frente

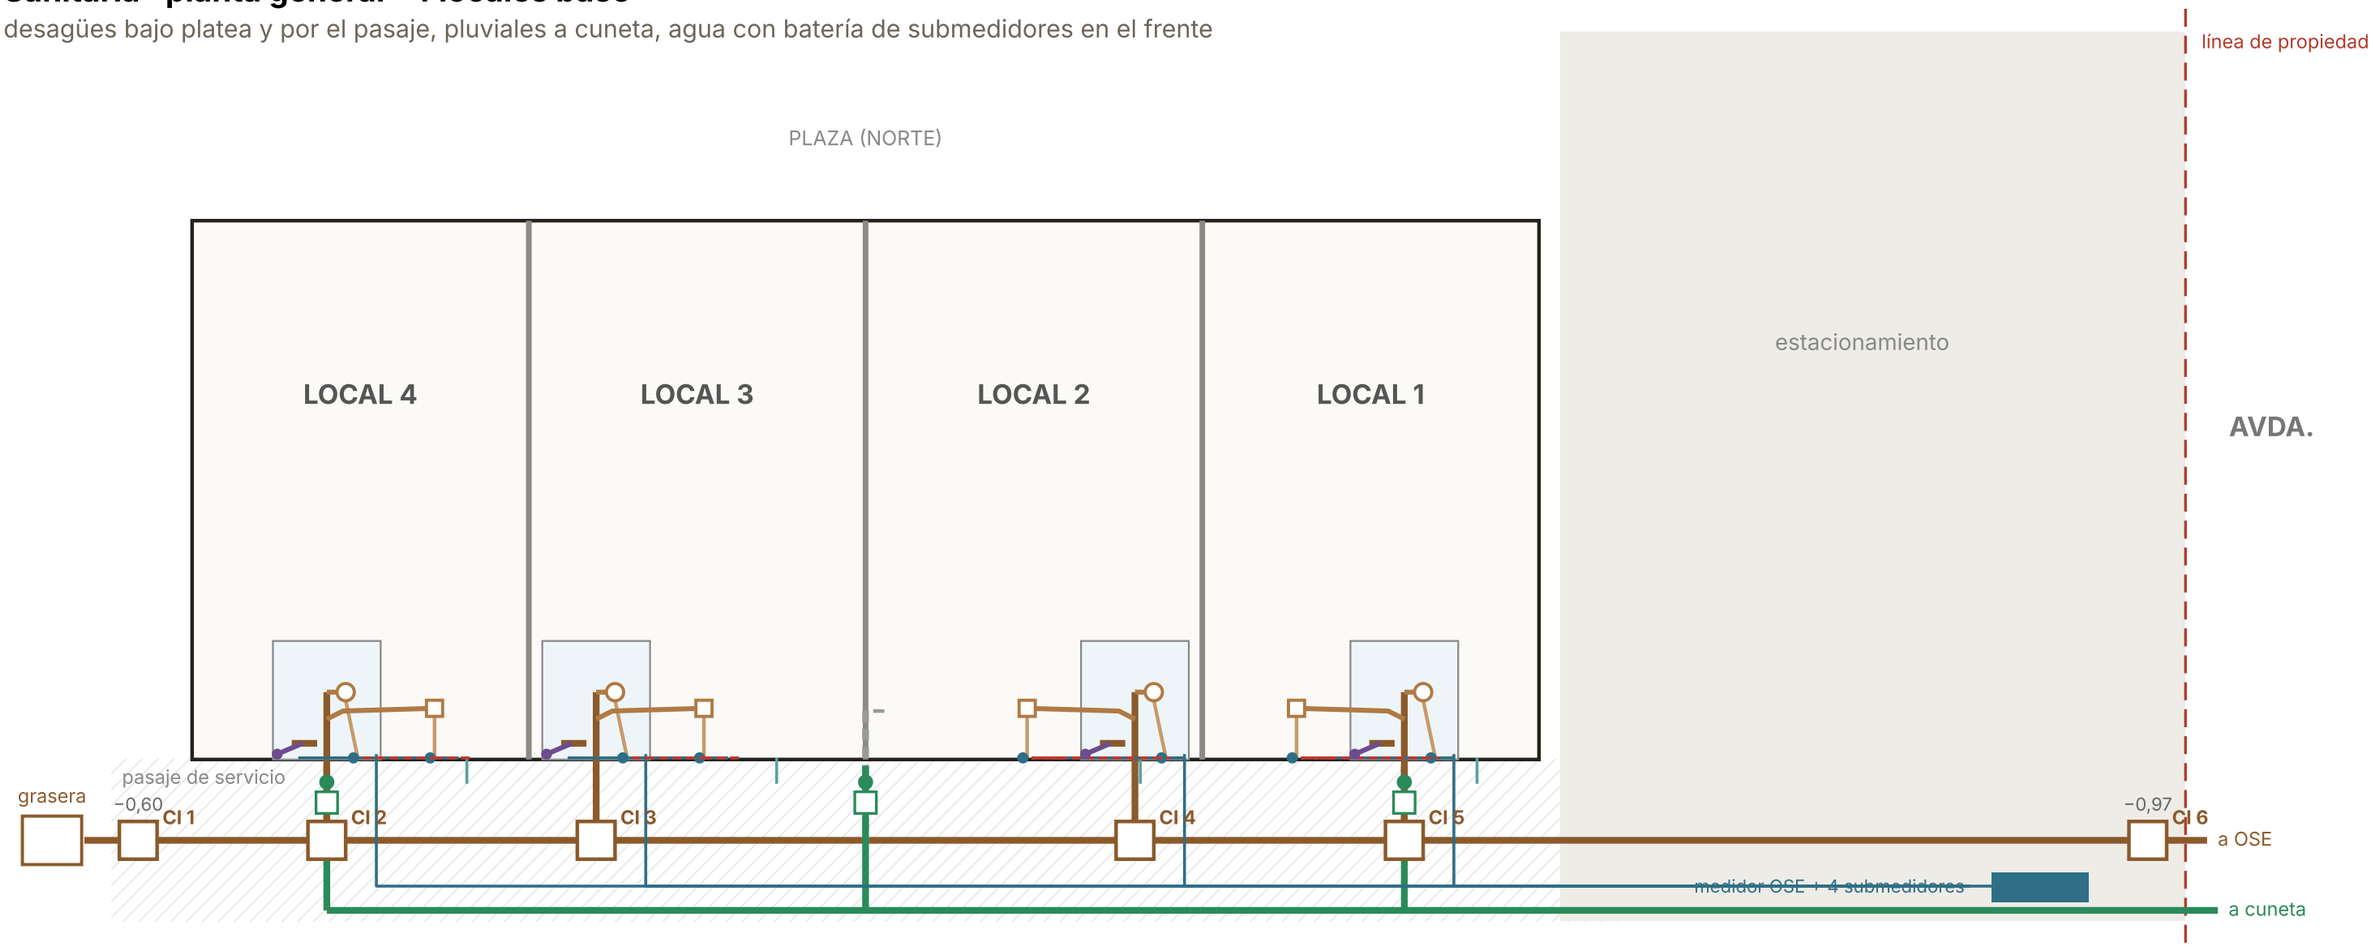


Colector Ø110 al 1 % con 6 cámaras · ramal de cada local a su cámara · previsiones sin usar con tapón · agua: un caño Ø25 por local desde su submedidor

cloacal Ø110 · Ø63 piletas · Ø40 · ventilación Ø63 · pluvial · agua fría · agua caliente · previsión sin usar (tapón)

PPS: pileta de patio sifonada abierta. PPT: pileta de patio tapada. CI: cámara de inspección, una por local sobre el colector. Colector a −0,60 en la CI 1 y −0,97 en la conexión.

Sanitaria: local tipo


LOCAL 3 · zona de servicio del local tipo (los otros iguales, a espejo si la cocina queda al oeste)

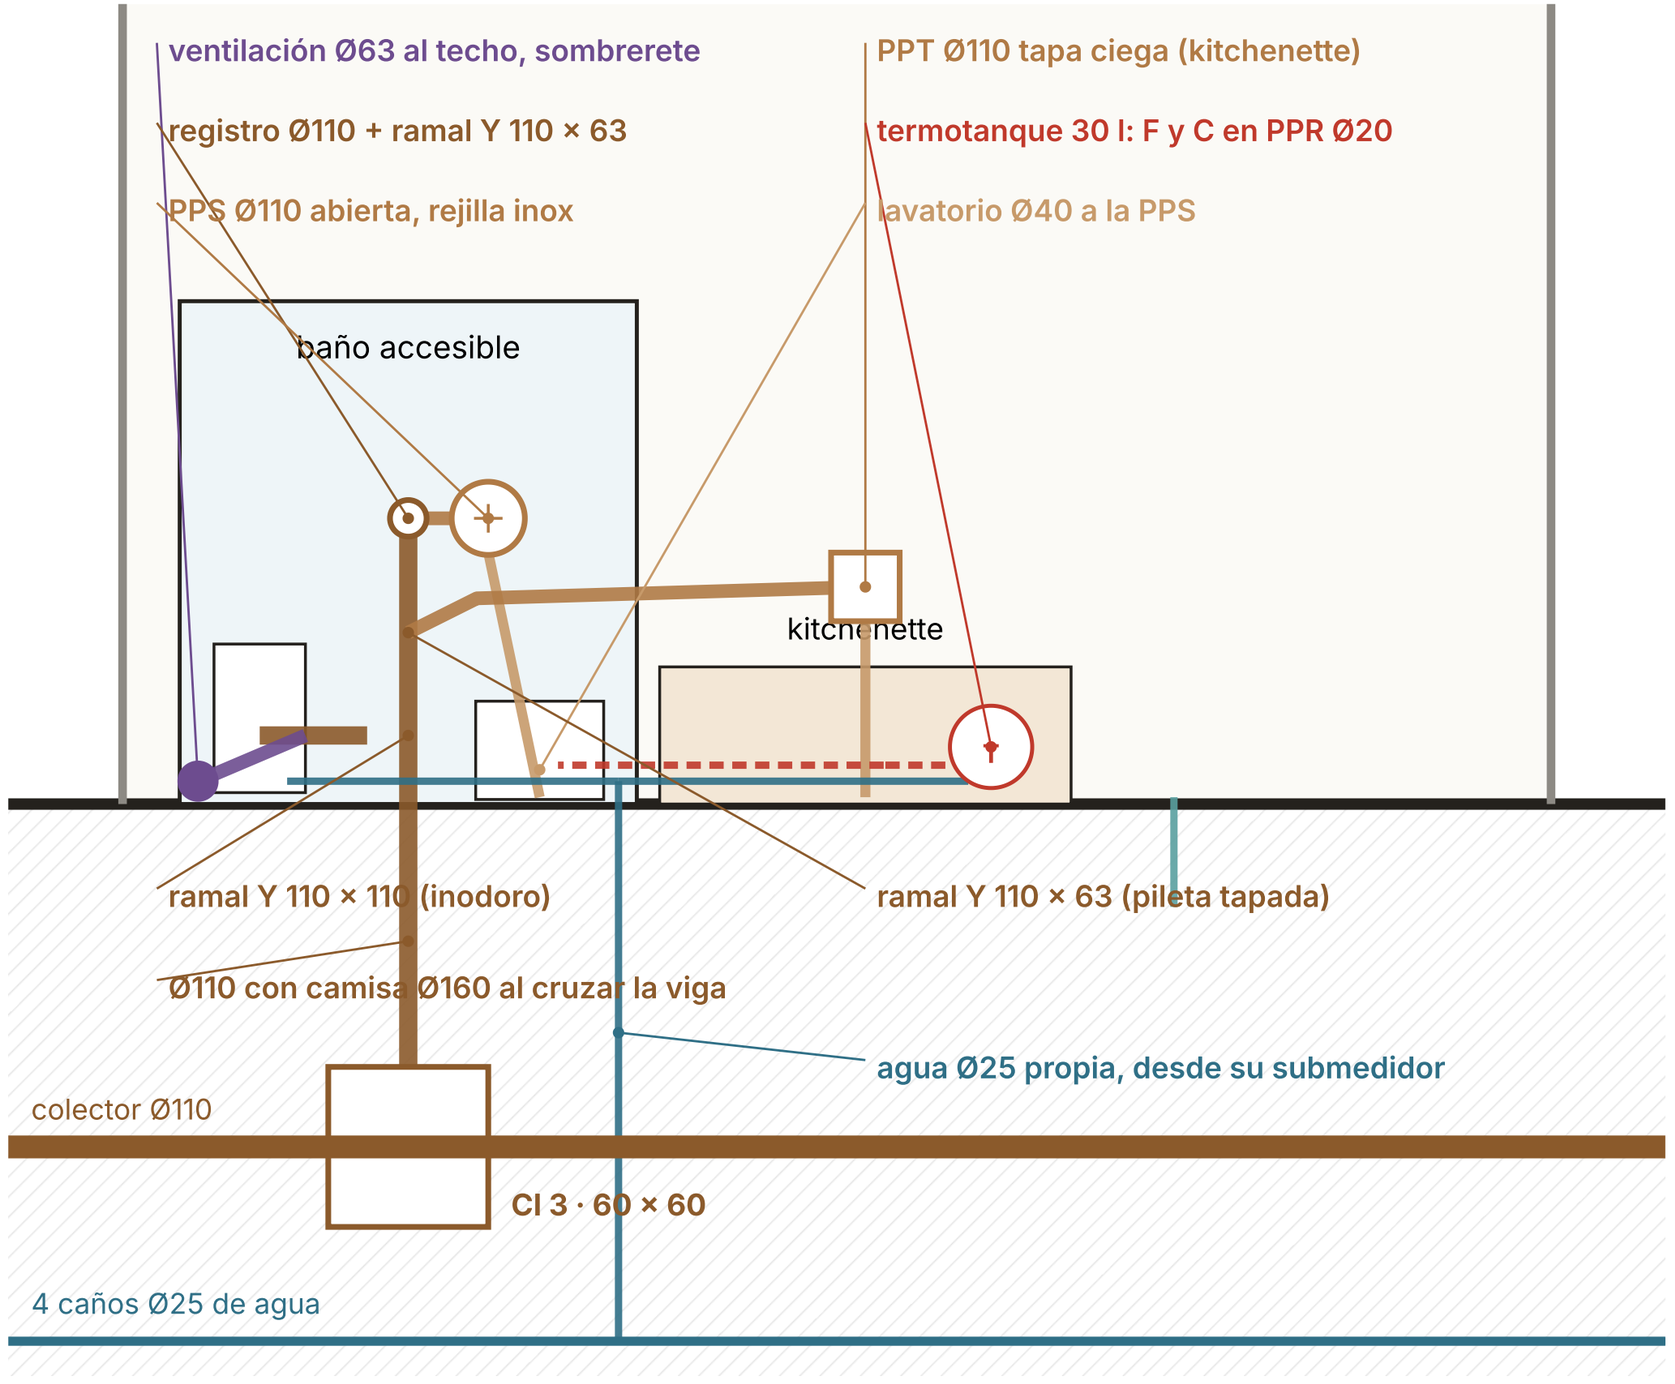

Eléctrica: planta general

Eléctrica · planta general · 4 locales base

gabinete de medidores en el frente, tableros de local (TD) junto al muro lateral, servicios comunes (TSC) en el pasaje

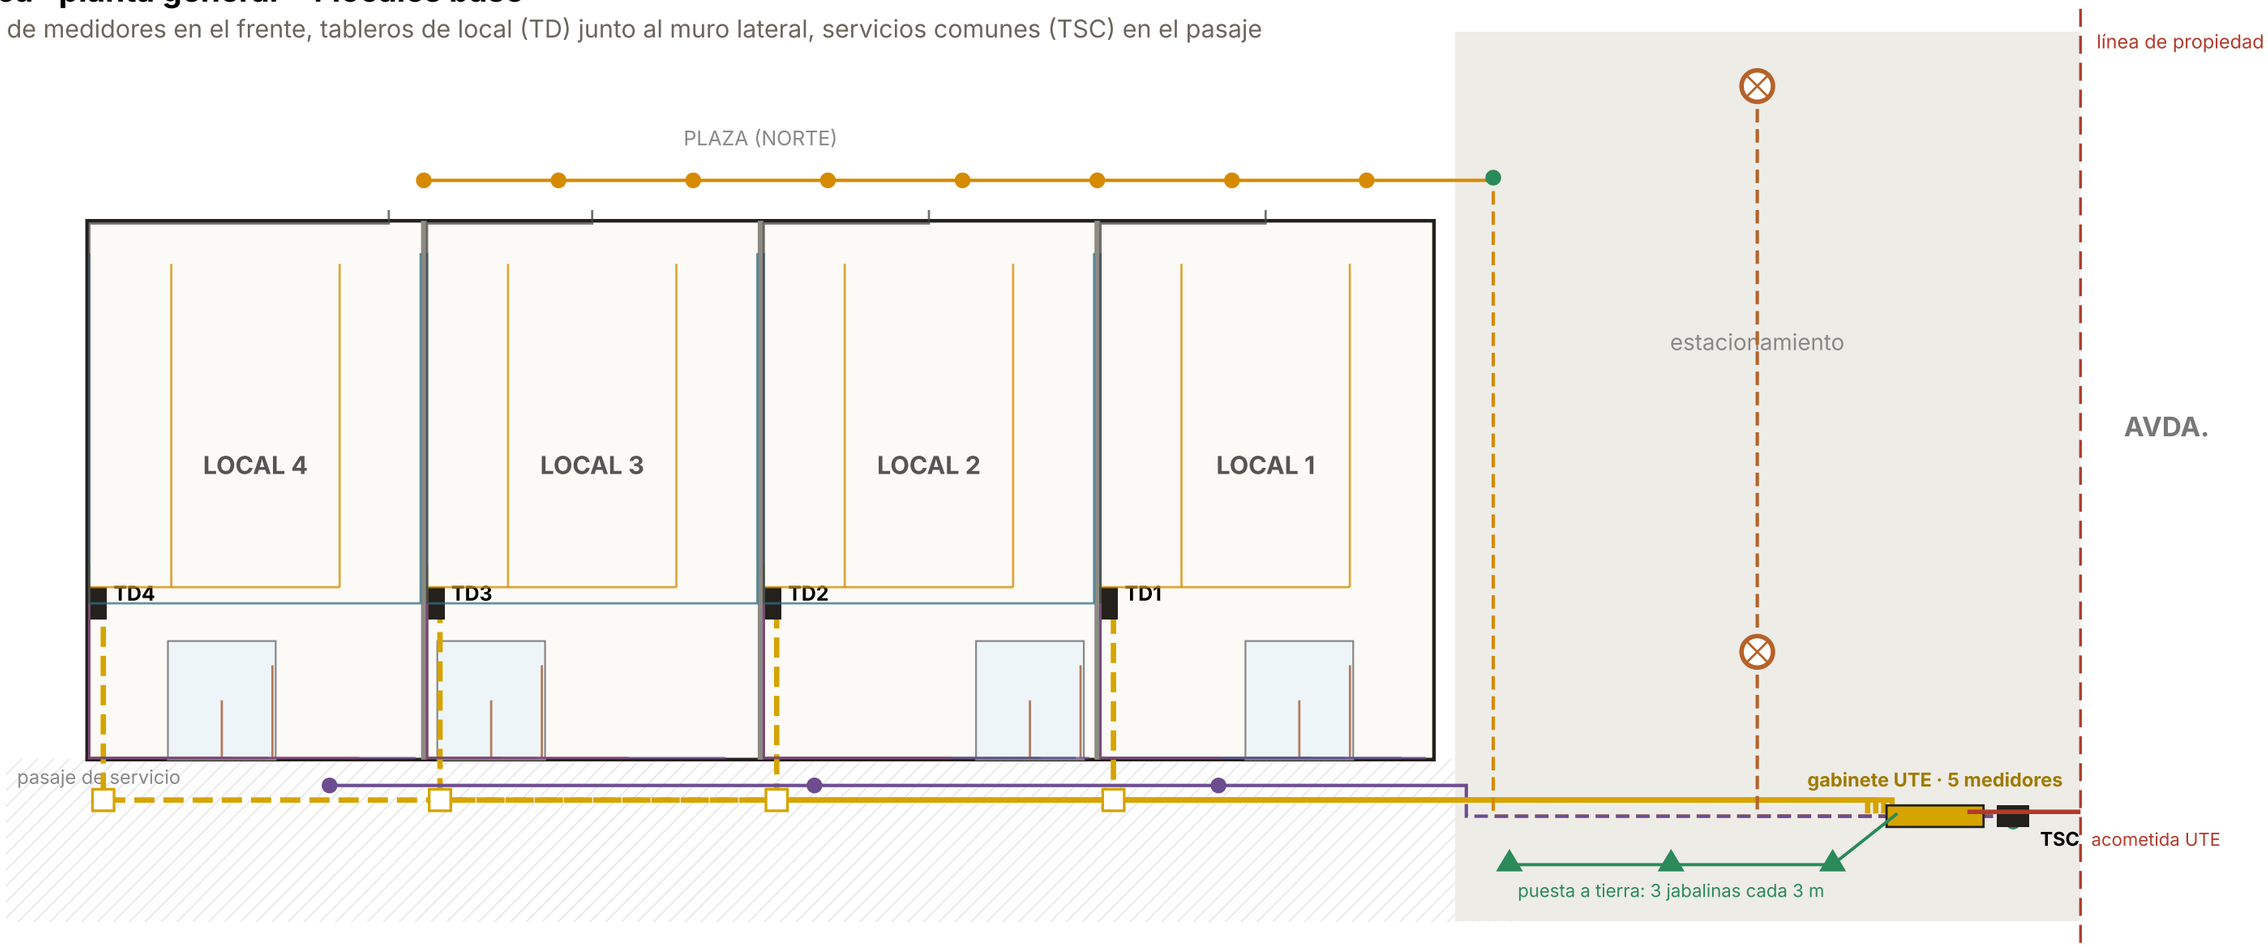


Alimentación monofásica 3 × 10 mm² en caño Ø50 enterrado, uno por local + uno de reserva · luces de plaza bajo la visera, 2 columnas en el estacionamiento y apliques en el pasaje

Medición monofásica por local en el gabinete de UTE del frente (hasta 9,2 kW), alimentación enterrada a cada tablero, servicios comunes en tablero aparte.

Eléctrica: local tipo

LOCAL 3 · local tipo 6,25 × 10,00

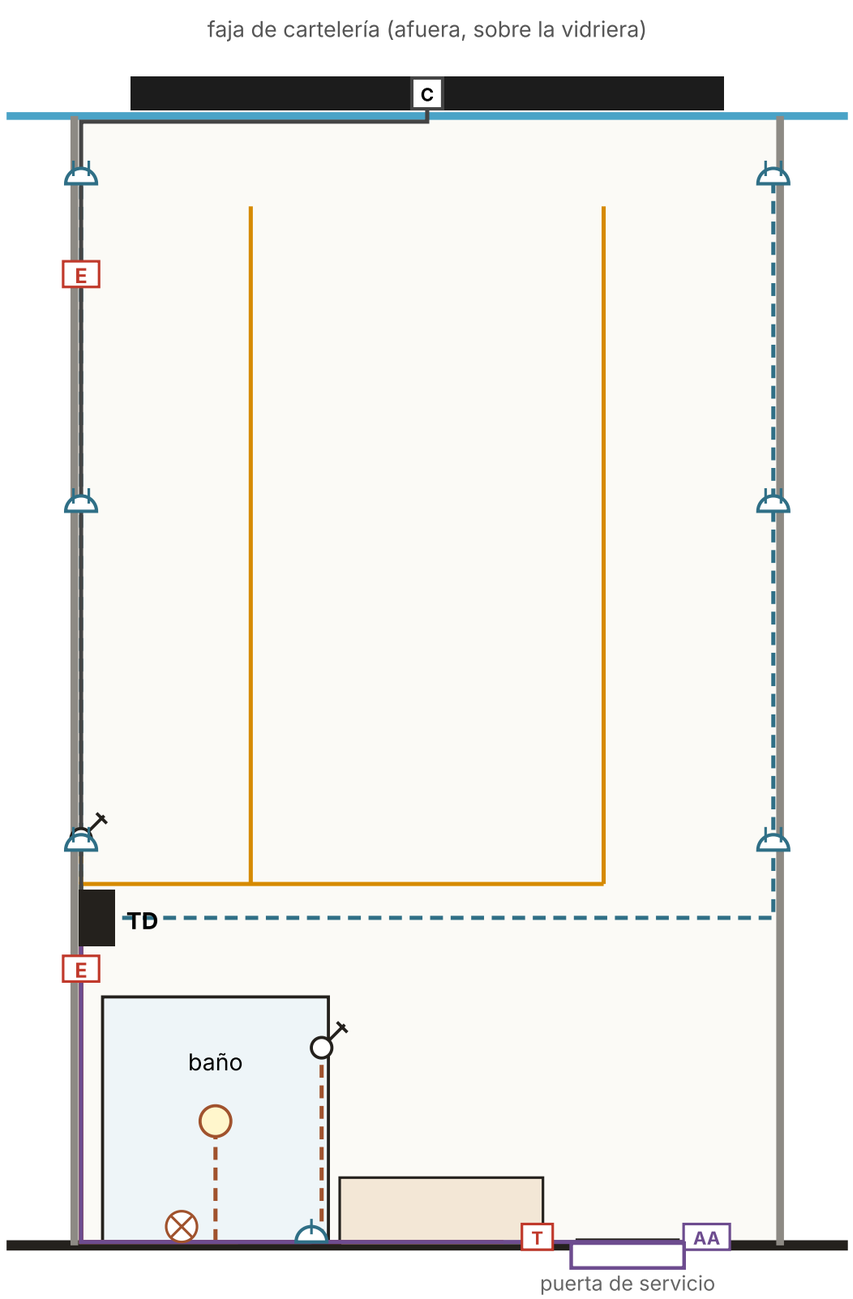

línea llena: caño rígido a la vista · punteada: corrugado dentro del divisorio

Circuitos

- C1 · Iluminación del salón: caños y cajas (las luminarias las elige el inquilino)
  1,5 mm² · 2 × 10 A · 23 m de caño
- C2 · Luz y extractor del baño
  1,5 mm² · 2 × 10 A · 10 m de caño
- C3 · Tomas del salón y del baño
  2,5 mm² · 2 × 16 A · 32 m de caño
- C5 · Termotanque
  2,5 mm² · 2 × 16 A · 7 m de caño
- C6 · Aire acondicionado
  4 mm² · 2 × 20 A · 9 m de caño
- C7 · Cartel en la faja (con reloj)
  2,5 mm² · 2 × 10 A · 12 m de caño


- luminaria LED lineal colgante
- E — luz de emergencia
- toma doble 10 A
- llave de 2 puntos
- AA — toma 20 A del aire
- T — salida termotanque
- C — caja estanca del cartel

Medición monofásica por local en el gabinete de UTE del frente (hasta 9,2 kW), alimentación enterrada a cada tablero, servicios comunes en tablero aparte.

Fachada norte (a la plaza)

Fachada norte (a la plaza)

como el render: la cenefa negra recorre todo el dintel y baja en la esquina del fondo; brise, faja con visera blanca, vidrieras y portal; todo a la misma altura

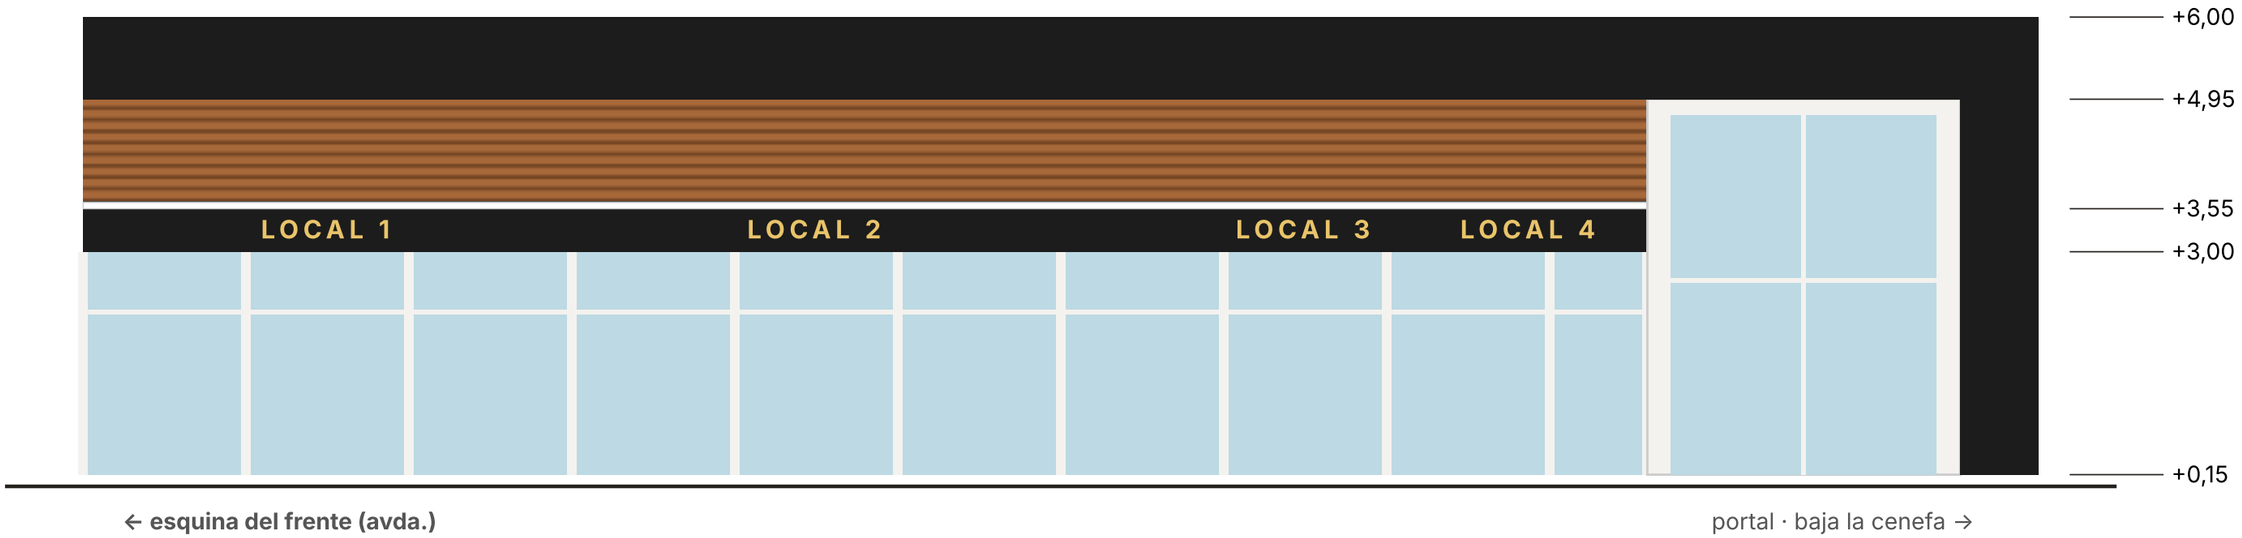


Alturas: piso terminado +0,15; vidriera hasta +3,00; faja de cartelería +3,00 a +3,50; visera blanca a +3,55; brise de +3,65 a +4,95; cenefa negra de +4,95 a +6,00, que es también el pretil. Toda la nave a la misma altura; el portal vidriado del extremo oeste va de piso a dintel. El techo cae hacia el sur (3 % engrafado o 7 % trapezoidal), a una canaleta interna escondida detrás del pretil.

Fachada este (a la avenida) y corte


Fachada este (a la avenida)

frente al terreno: la cenefa sube en la esquina sur y corre por arriba; vidriera, faja y brise dan la

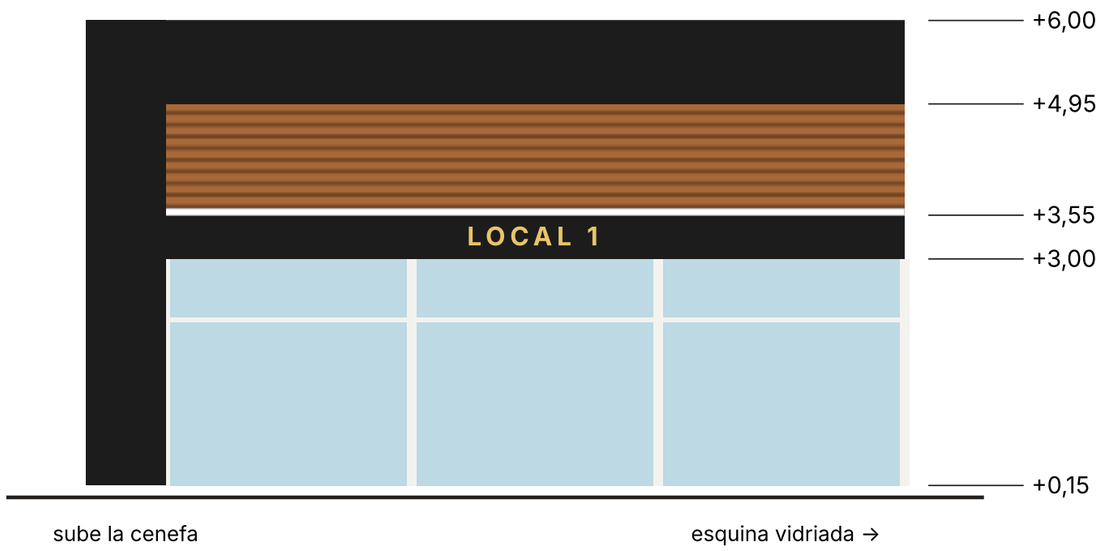

Corte transversal A-B

Isodec PIR 80 mm engrafado, grafito sobre correas · pórtico IPE

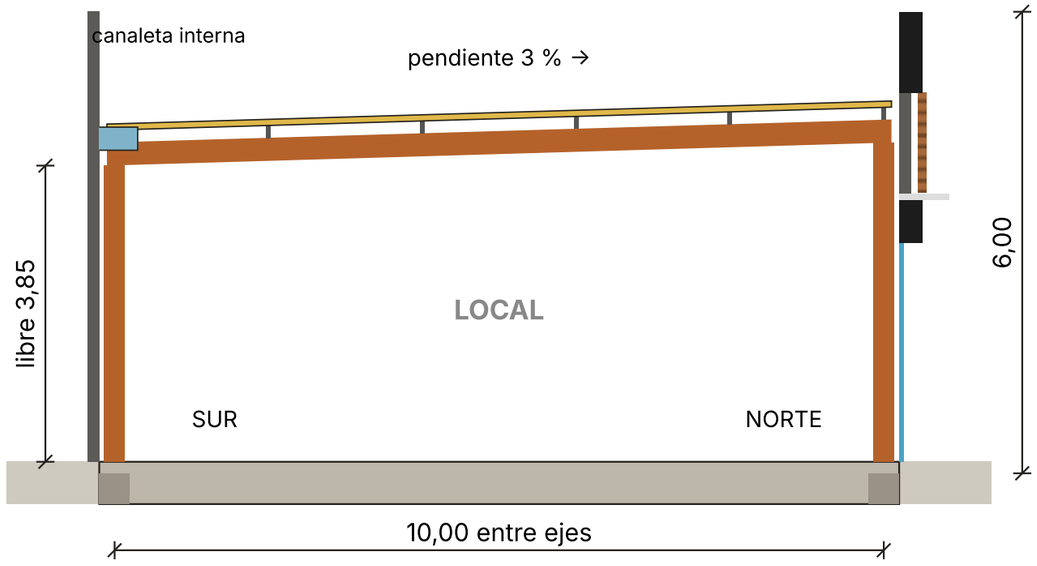


Alturas: piso terminado +0,15; vidriera hasta +3,00; faja de cartelería +3,00 a +3,50; visera blanca a +3,55; brise de +3,65 a +4,95; cenefa negra de +4,95 a +6,00, que es también el pretil. Toda la nave a la misma altura; el portal vidriado del extremo oeste va de piso a dintel. El techo cae hacia el sur (3 % engrafado o 7 % trapezoidal), a una canaleta interna escondida detrás del pretil.

Detalle del frente norte: cenefa, brise y faja

Detalle del frente norte: cenefa, brise y faja

corte por la fachada a la plaza · escala aproximada 1:20

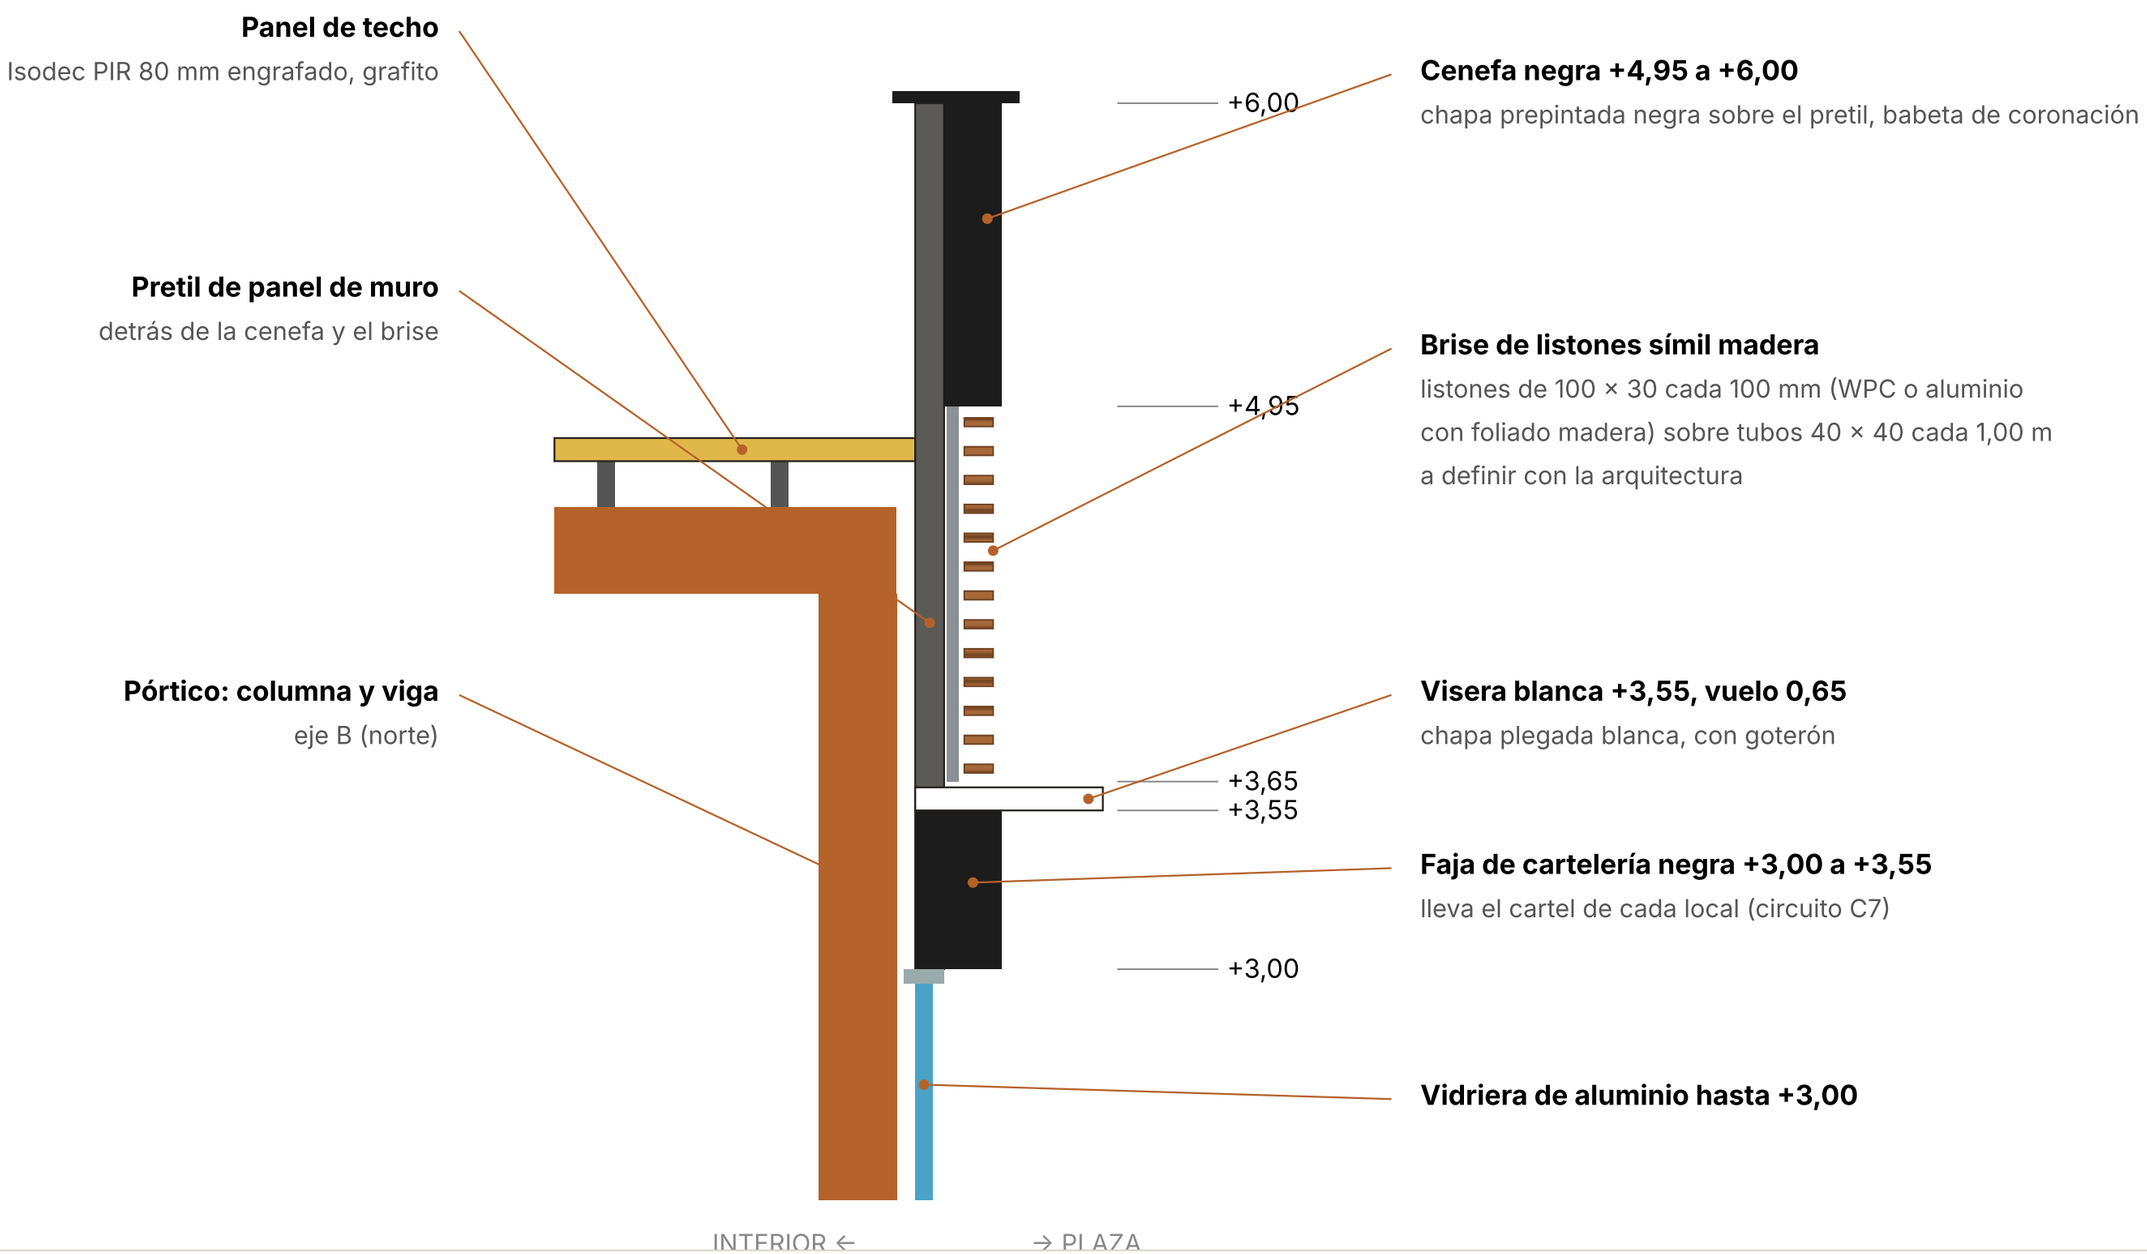

Alturas: piso terminado +0,15; vidriera hasta +3,00; faja de cartelería +3,00 a +3,50; visera blanca a +3,55; brise de +3,65 a +4,95; cenefa negra de +4,95 a +6,00, que es también el pretil. Toda la nave a la misma altura; el portal vidriado del extremo oeste va de piso a dintel. El techo cae hacia el sur (3 % engrafado o 7 % trapezoidal), a una canaleta interna escondida detrás del pretil.

Render del anteproyecto (enviado por el cliente)

