

SMART BUILDING URUGUAY

Locales comerciales Avda. Pedragosa Sierra

Padrón 10596 · Punta del Este, Maldonado

Material de base para el proyecto ejecutivo y el permiso de construcción
Para: Arq. Pablo Alcoba · 13 de noviembre de 2026

Programa	4 locales comerciales en cáscara + baño, planta de 25 × 10 m (250 m²), sin columnas interiores
Estructura	Pórticos metálicos cada 5 m, platea H30 con vigas de fundación (cálculo: Ing. Ricardo Portugau)
Envolvente	Todo en panel PIR blanco (muros lisos y techo Isodec engrafado), elegido por las hormigas; vidriera continua a la plaza, faja, brise símil madera y cenefa negra
Obra	SBU · Ramiro Portugau, director de obra


Láminas

1. Implantación: planta completa con el terreno
2. Planta de arquitectura
3. Sanitaria: planta general
4. Sanitaria: local tipo
5. Eléctrica: planta general
6. Eléctrica: local tipo
7. Fachada norte (a la plaza)
8. Fachada este (a la avenida) y corte
9. Detalle del frente: cenefa, brise símil madera y faja
10. Detalle del borde sur: canaleta, bajadas y desborde
11. Render del anteproyecto (del cliente)

Implantación: planta completa con el terreno

Implantación · padrón 10596


escala gráfica: 1 m = 22 px · FOS 25 % · 6 estacionamientos (pide 3)

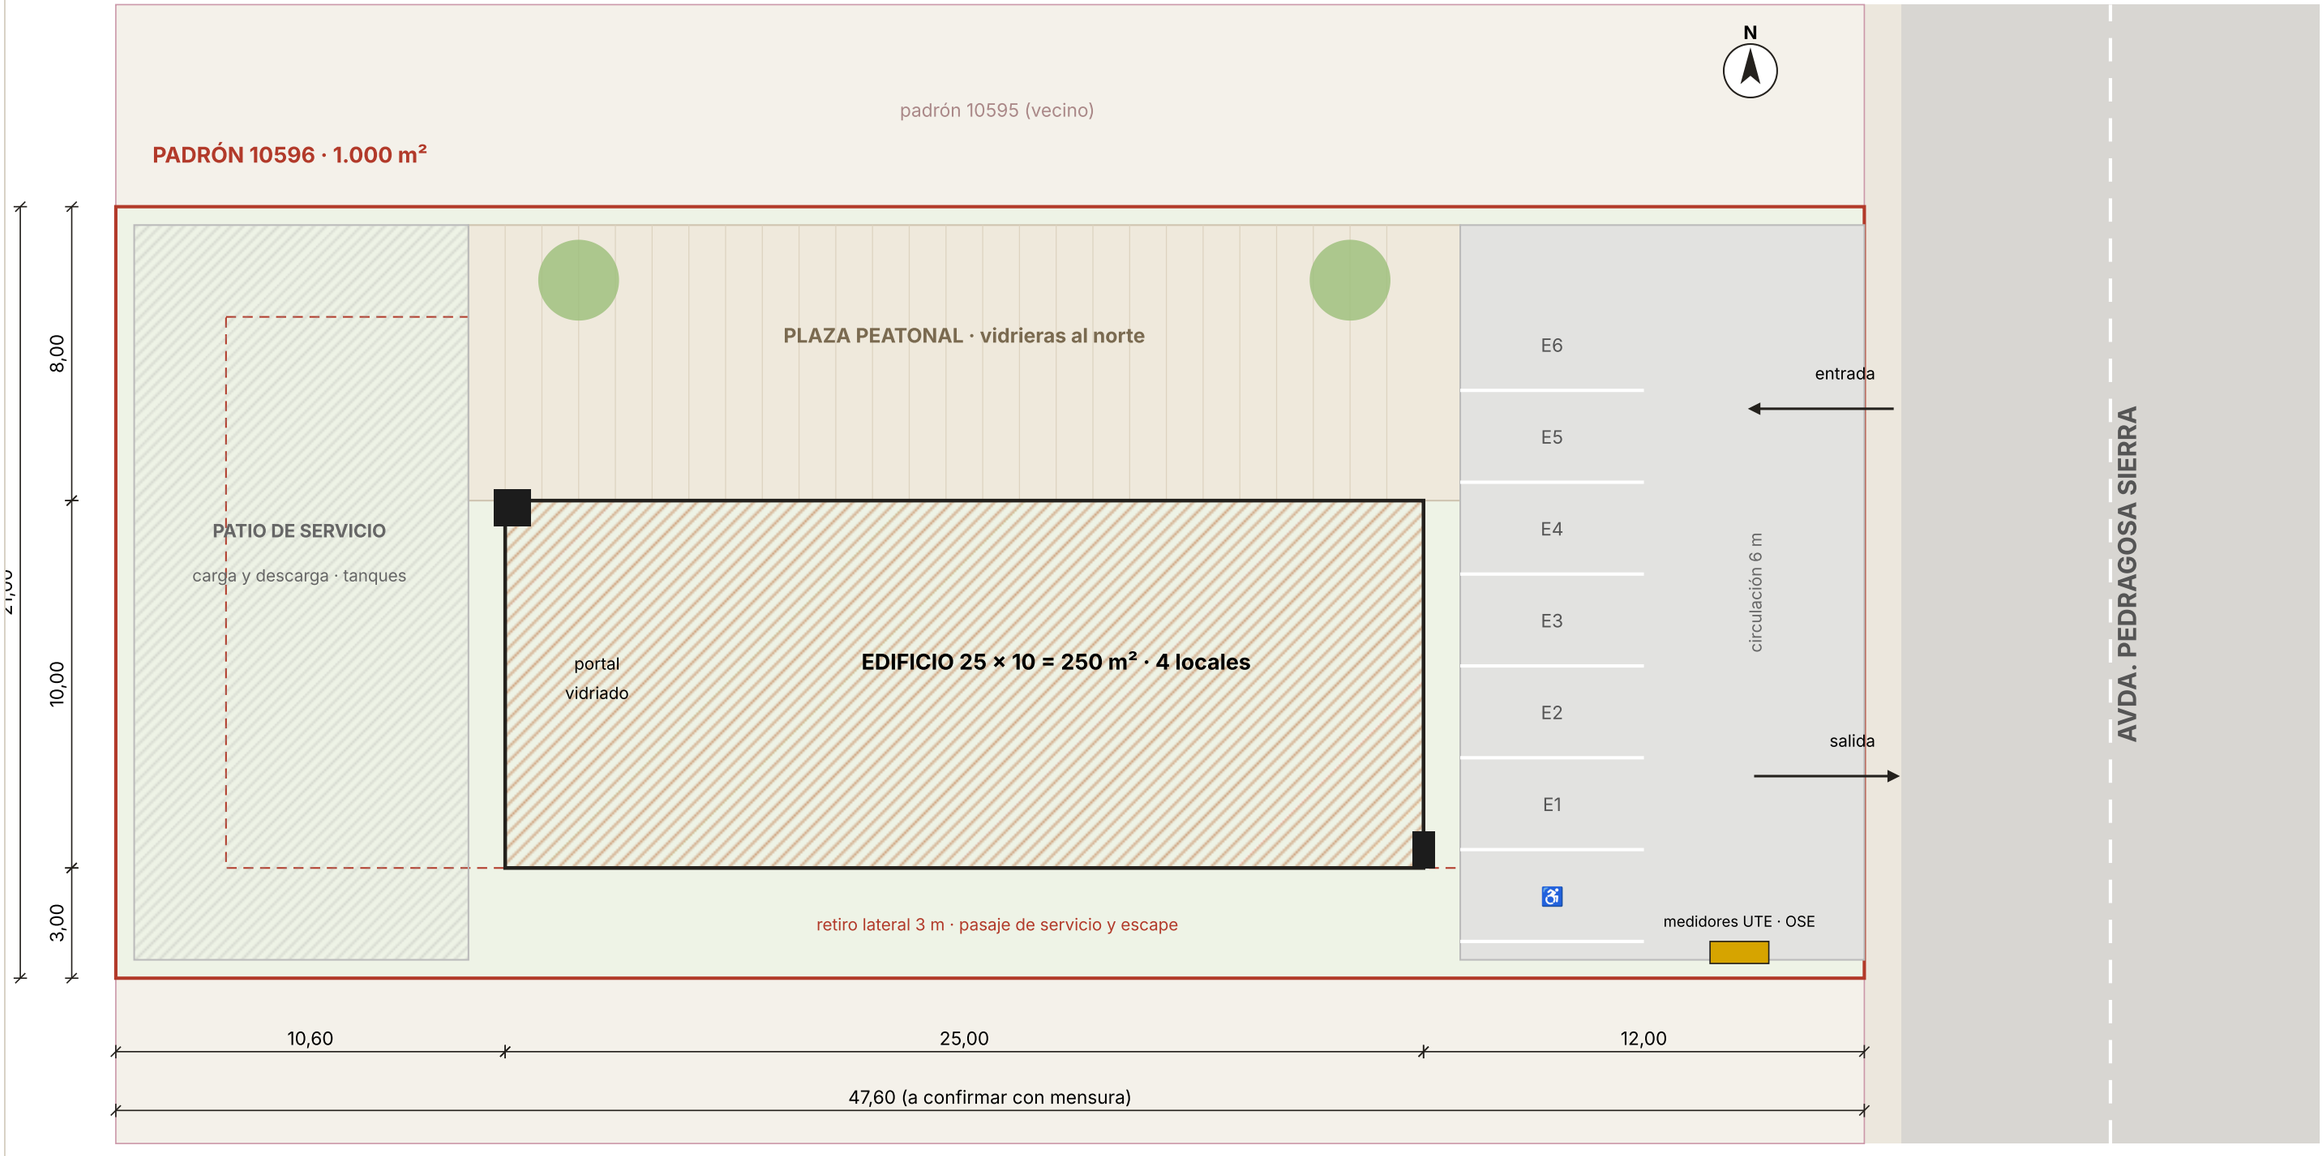

Planta de arquitectura

Planta · 4 locales


ejes cada 5 m · luz libre 10 m · cotas parciales y acumuladas desde el eje 1

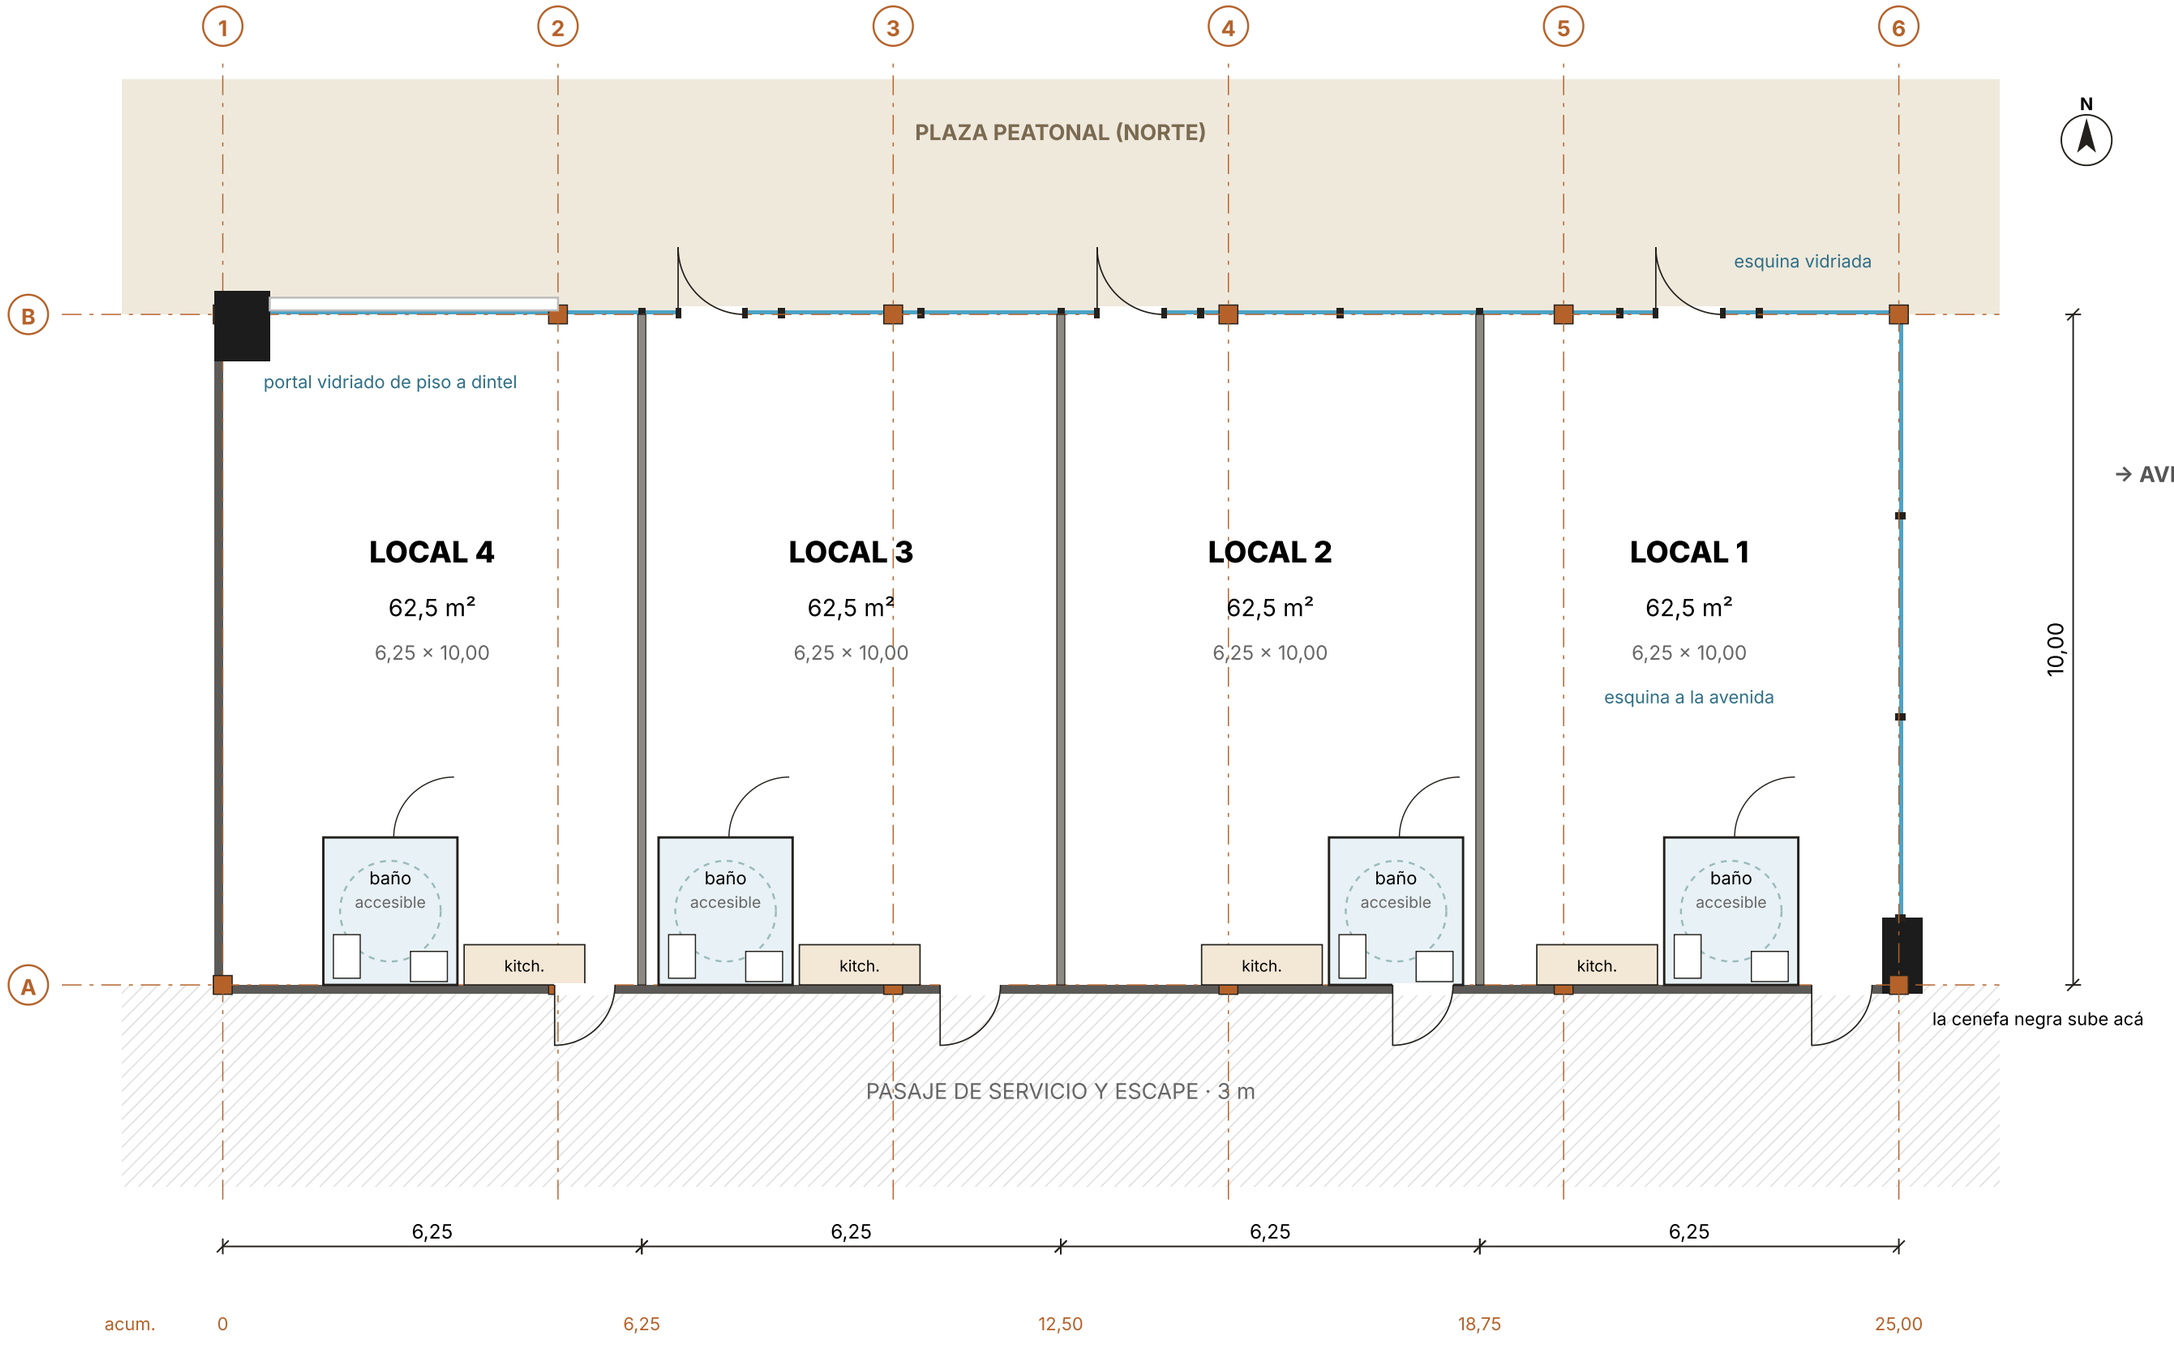

Sanitaria: planta general

Sanitaria · planta general · 4 locales base

desagües bajo platea y por el pasaje, pluviales a cuneta, agua con batería de submedidores en el frente

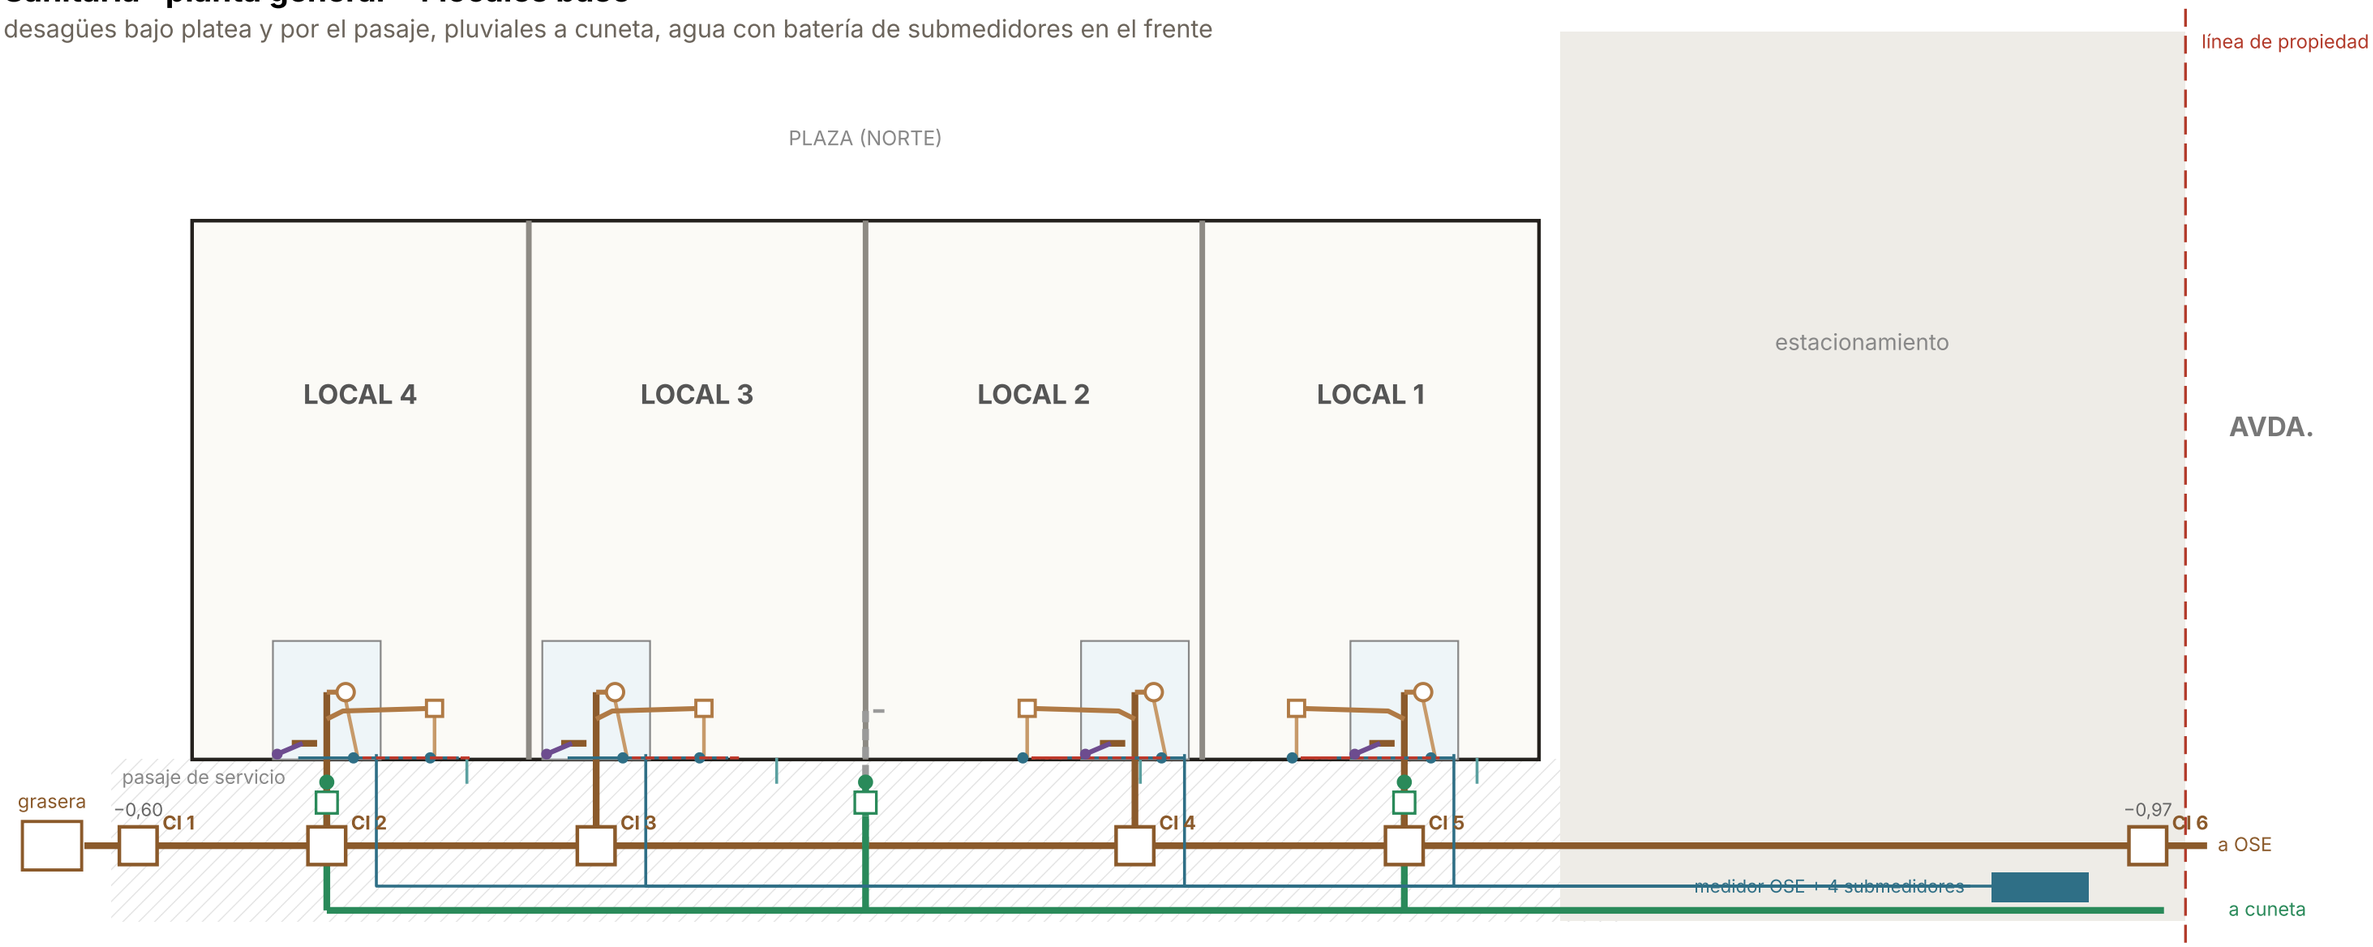


Colector Ø110 al 1 % con 6 cámaras · ramal de cada local a su cámara · previsiones sin usar con tapón · agua: un caño Ø25 por local desde su submedidor

cloacal Ø110 · Ø63 piletas · Ø40 · ventilación Ø63 · pluvial · agua fría · agua caliente · previsión sin usar (tapón)

PPS: pileta de patio sifonada abierta. PPT: pileta de patio tapada. CI: cámara de inspección, una por local sobre el colector. Colector a −0,60 en la CI 1 y −0,97 en la conexión.

Sanitaria: local tipo


LOCAL 3 · zona de servicio del local tipo (los otros iguales, a espejo si la cocina queda al oeste)

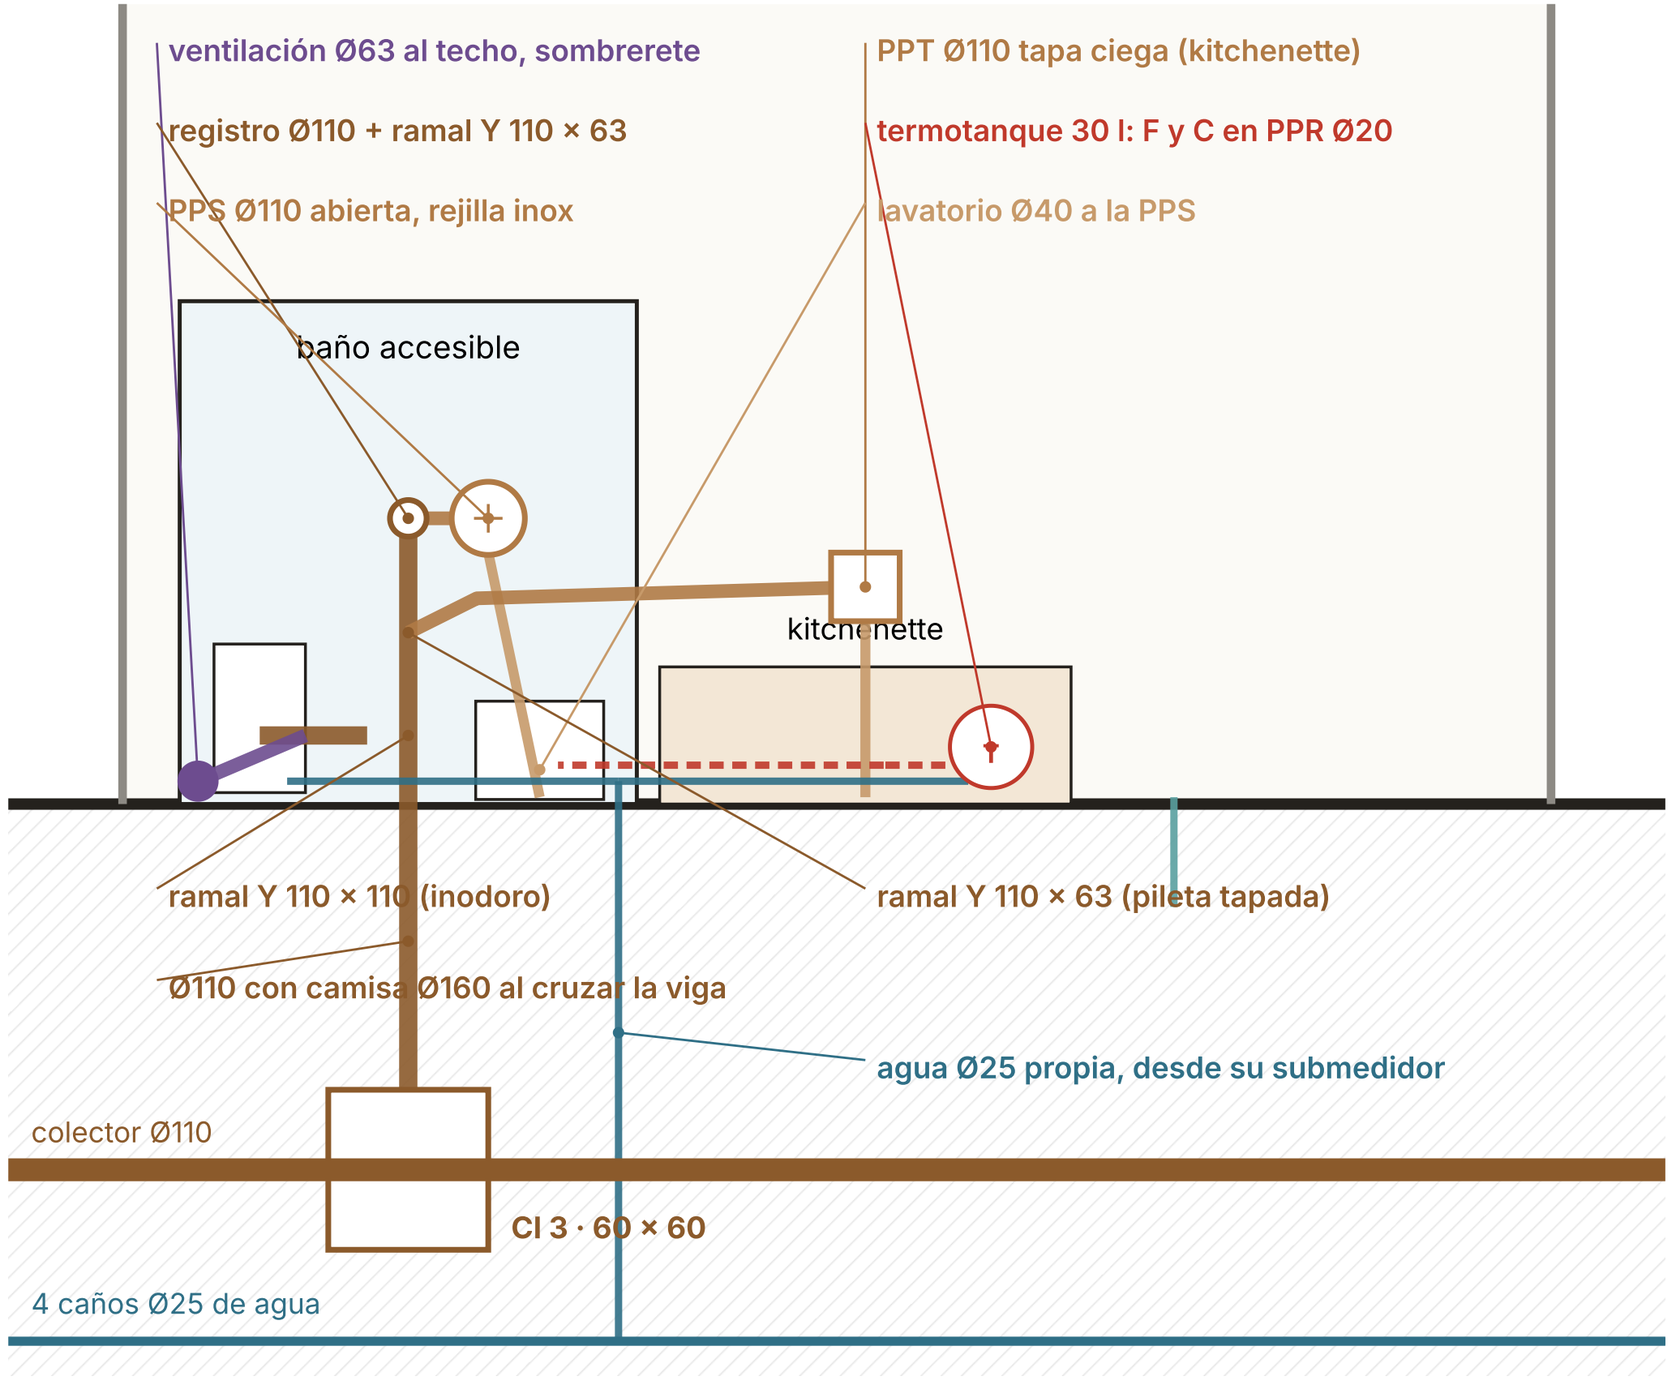

Eléctrica: planta general

Eléctrica · planta general · 4 locales base

gabinete de medidores en el frente, tableros de local (TD) junto al muro lateral, servicios comunes (TSC) en el pasaje

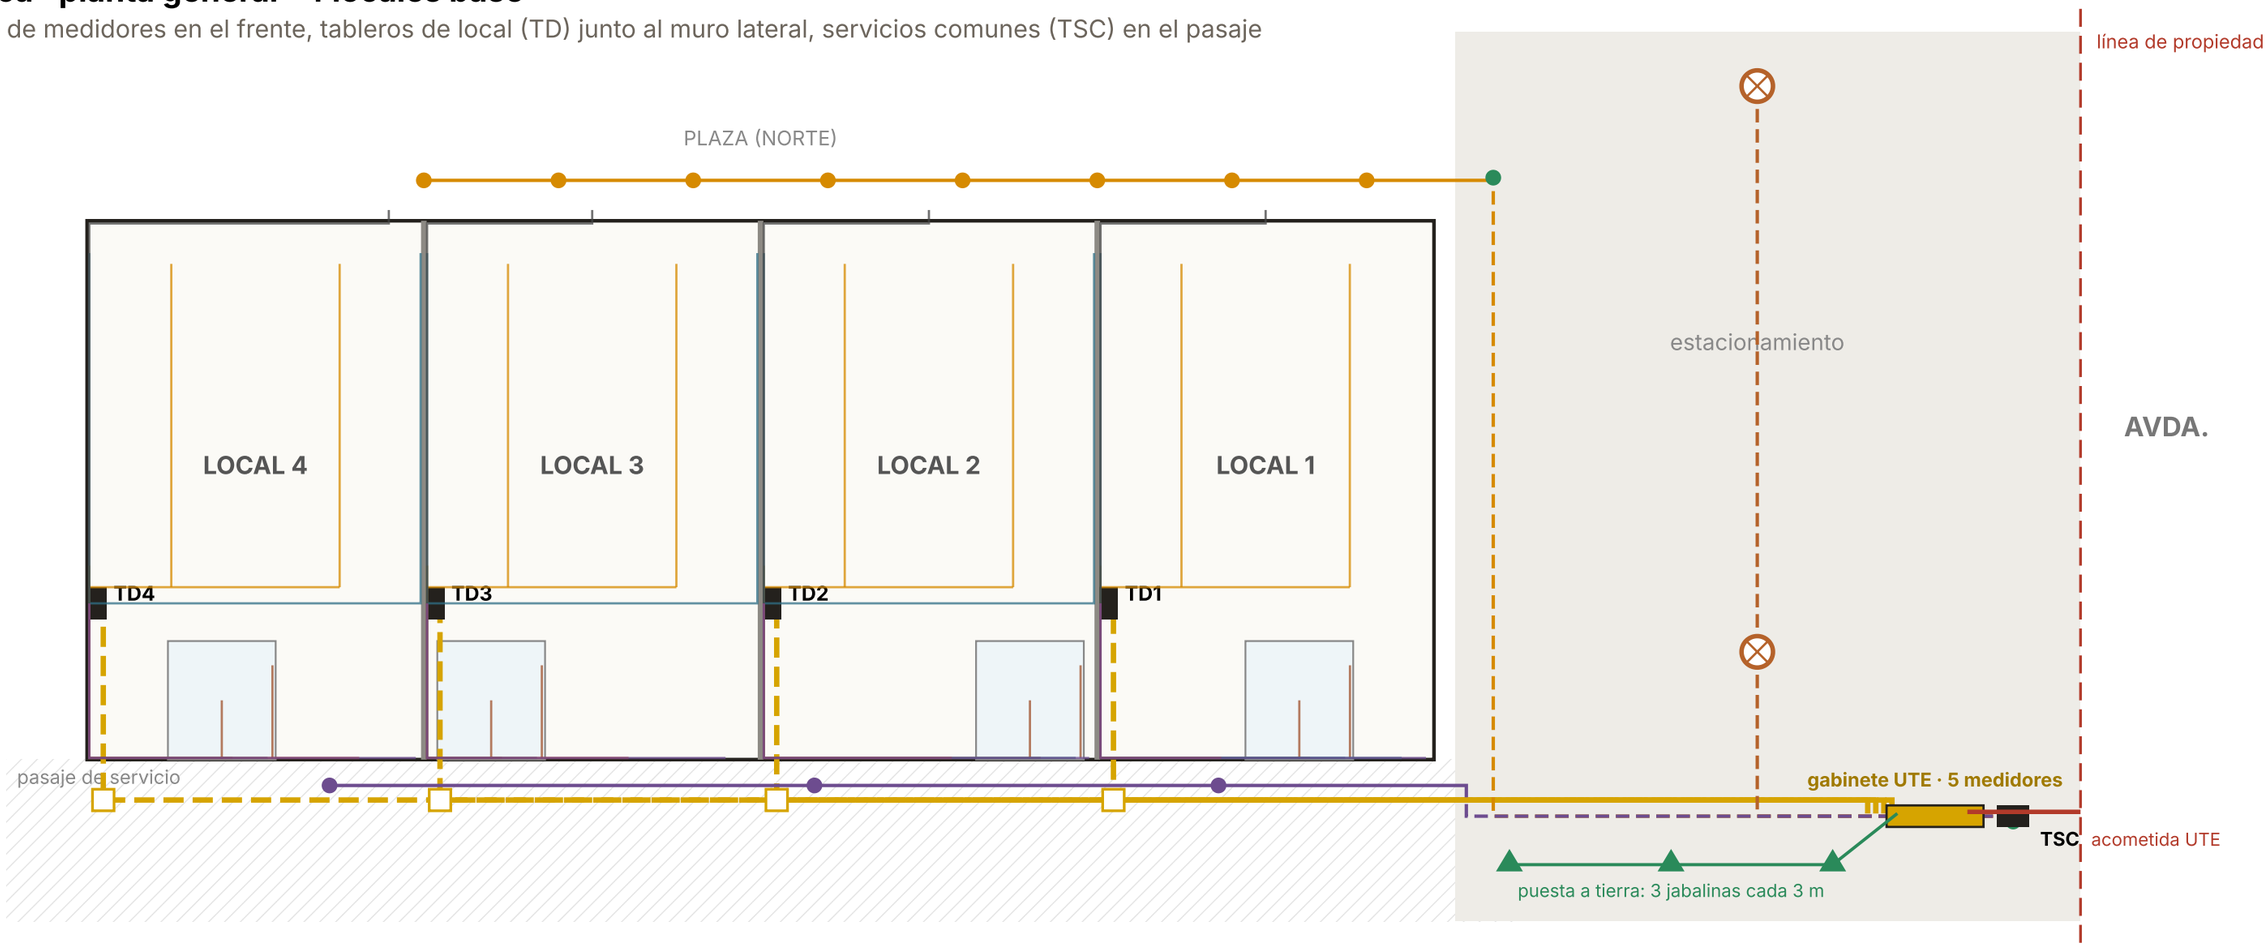


Alimentación monofásica 3 × 10 mm² en caño Ø50 enterrado, uno por local + uno de reserva · luces de plaza bajo la visera, 2 columnas en el estacionamiento y apliques en el pasaje

Medición monofásica por local en el gabinete de UTE del frente (hasta 9,2 kW), alimentación enterrada a cada tablero, servicios comunes en tablero aparte.

Eléctrica: local tipo

LOCAL 3 · local tipo 6,25 × 10,00

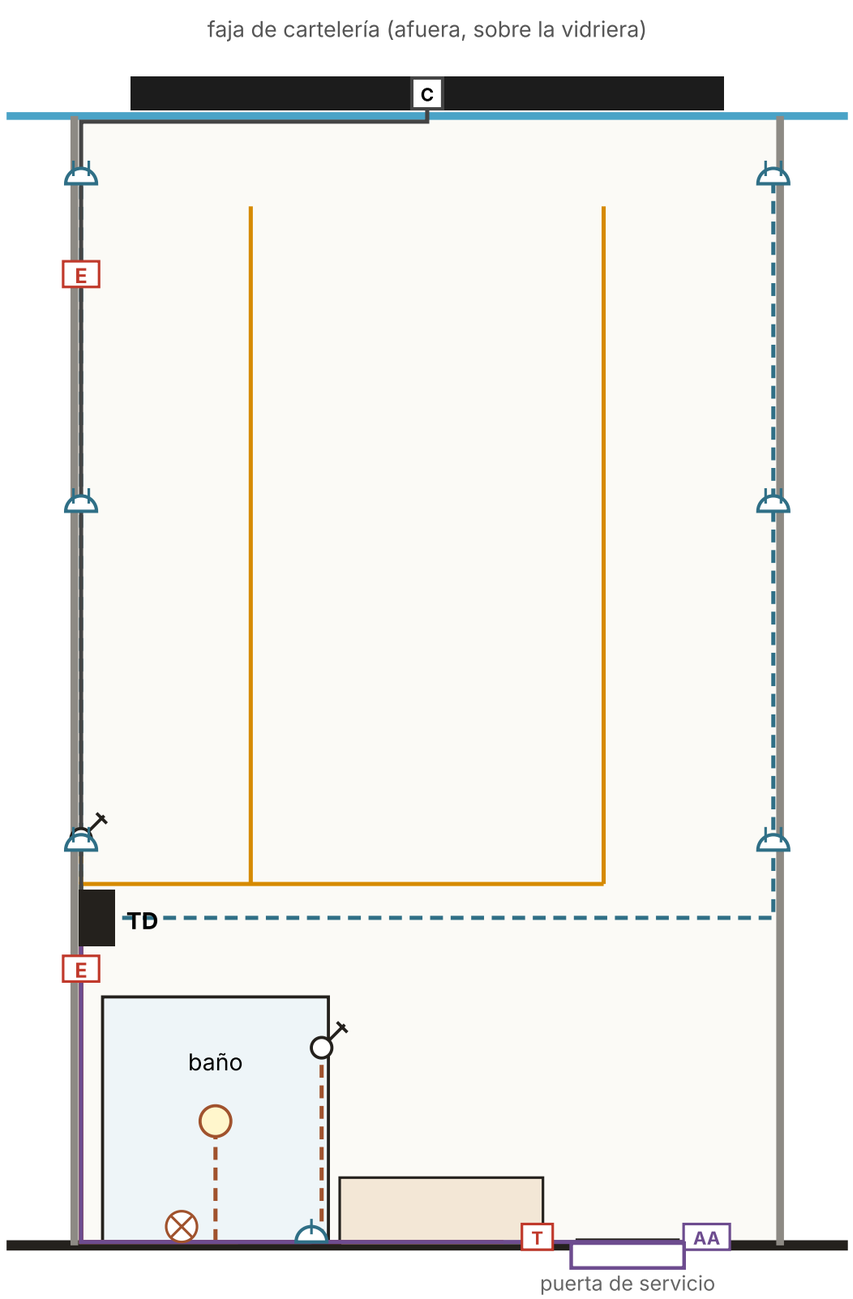

línea llena: caño rígido a la vista · punteada: corrugado dentro del divisorio

Circuitos

- C1 · Iluminación del salón: caños y cajas (las luminarias las elige el inquilino)
  1,5 mm² · 2 × 10 A · 23 m de caño
- C2 · Luz y extractor del baño
  1,5 mm² · 2 × 10 A · 10 m de caño
- C3 · Tomas del salón y del baño
  2,5 mm² · 2 × 16 A · 32 m de caño
- C5 · Termotanque
  2,5 mm² · 2 × 16 A · 7 m de caño
- C6 · Aire acondicionado
  4 mm² · 2 × 20 A · 9 m de caño
- C7 · Cartel en la faja (con reloj)
  2,5 mm² · 2 × 10 A · 12 m de caño


- luminaria LED lineal colgante
- E — luz de emergencia
- toma doble 10 A
- llave de 2 puntos
- AA — toma 20 A del aire
- T — salida termotanque
- C — caja estanca del cartel

Medición monofásica por local en el gabinete de UTE del frente (hasta 9,2 kW), alimentación enterrada a cada tablero, servicios comunes en tablero aparte.

Fachada norte (a la plaza)

Fachada norte (a la plaza)

como el render: la cenefa negra recorre todo el dintel y baja en la esquina del fondo; brise, faja con visera blanca, vidrieras y portal; todo a la misma altura

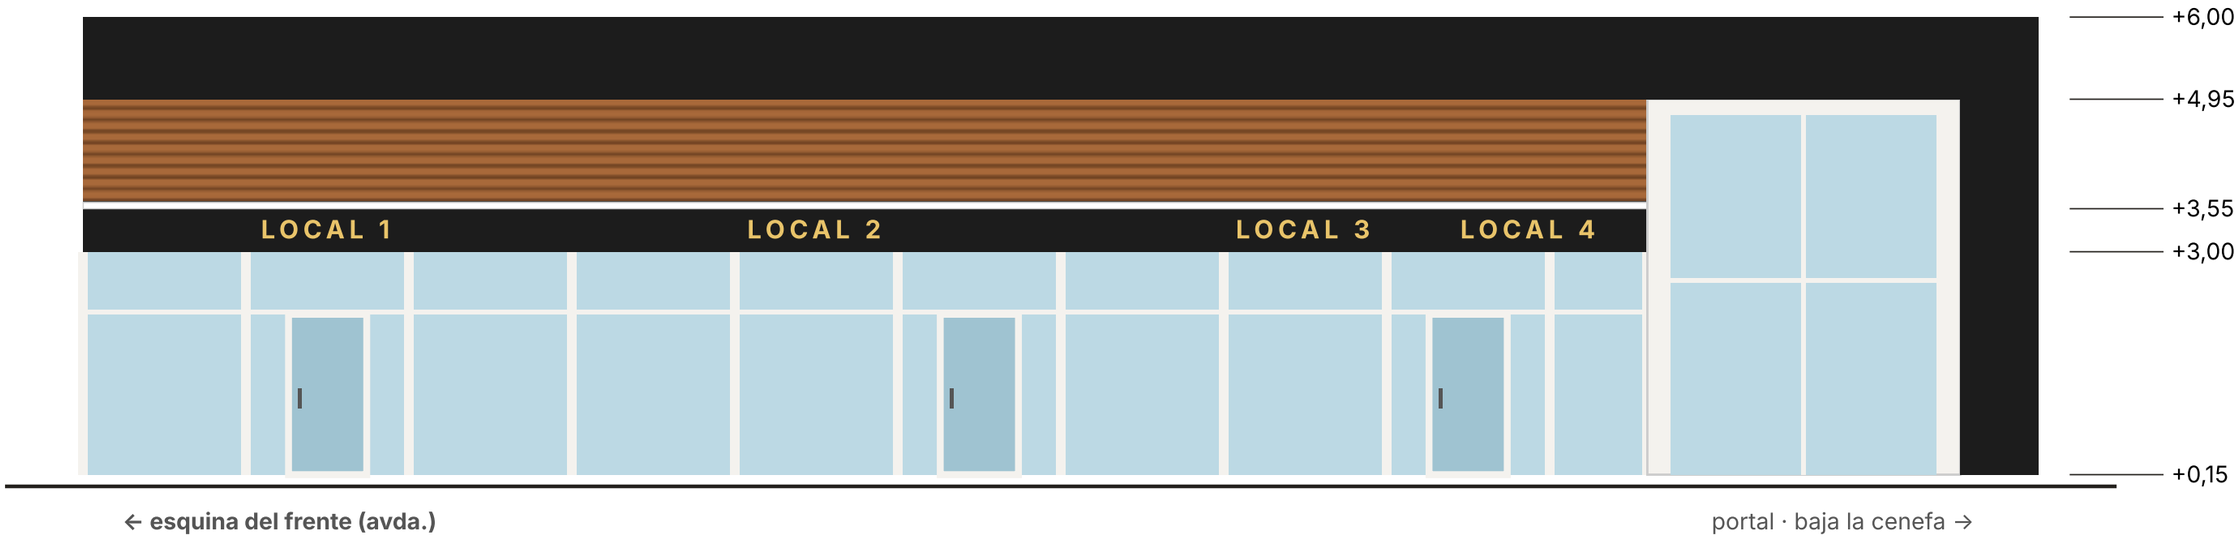


Alturas: piso terminado +0,15; vidriera hasta +3,00; faja de cartelería +3,00 a +3,50; visera blanca a +3,55; brise de +3,65 a +4,95; cenefa negra de +4,95 a +6,00, que es también el pretil. Toda la nave a la misma altura; el portal vidriado del extremo oeste va de piso a dintel. El techo cae hacia el sur (3 % engrafado o 7 % trapezoidal), a una canaleta interna escondida detrás del pretil.

Fachada este (a la avenida) y corte


Fachada este (a la avenida)

frente al terreno: la cenefa sube en la esquina sur y corre por arriba; vidriera, faja y brise dan la

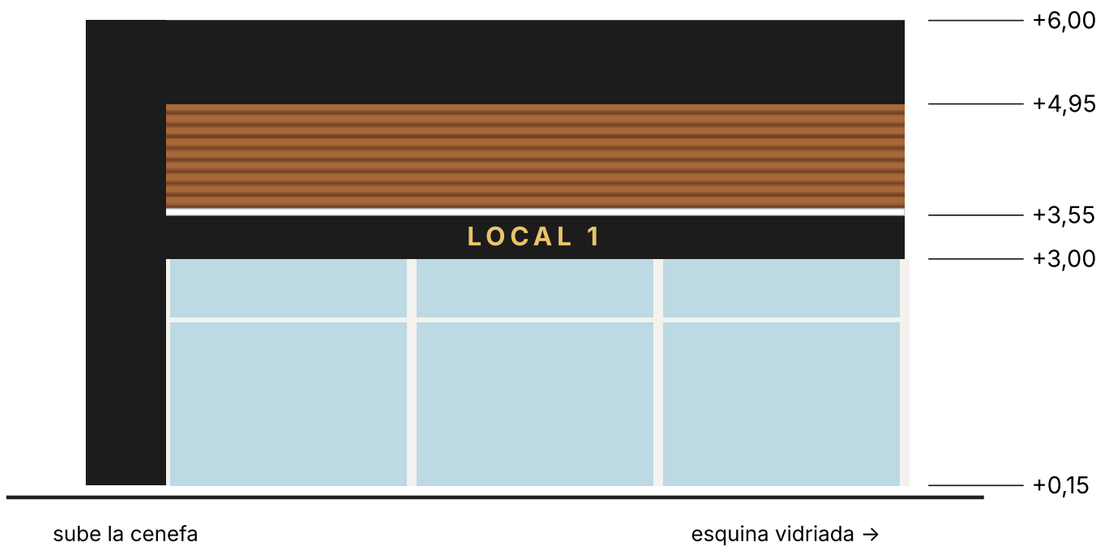

Corte transversal A-B

Isodec PIR 80 mm engrafado, blanco sobre correas · pórtico IPE

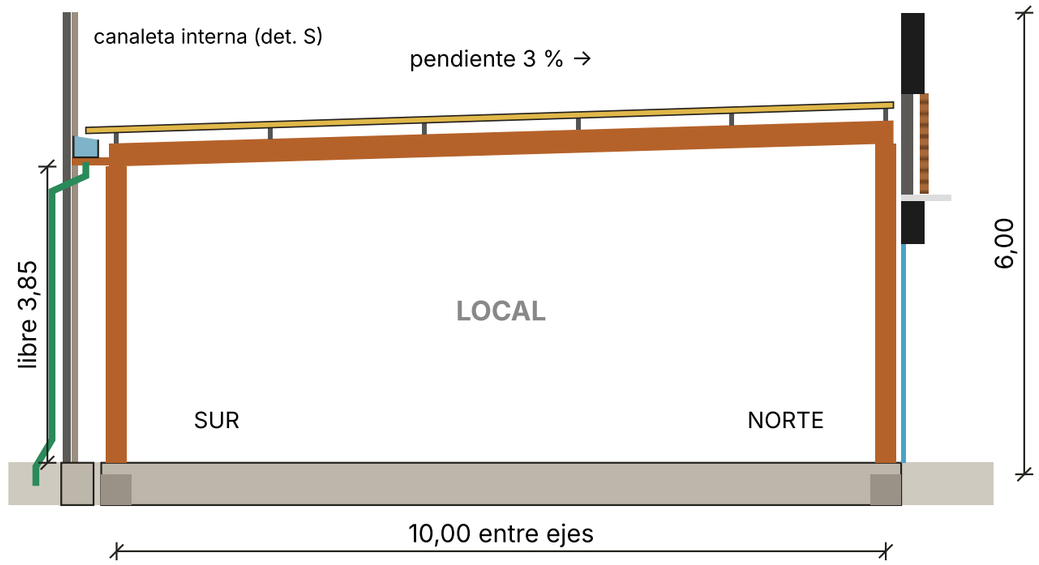


Alturas: piso terminado +0,15; vidriera hasta +3,00; faja de cartelería +3,00 a +3,50; visera blanca a +3,55; brise de +3,65 a +4,95; cenefa negra de +4,95 a +6,00, que es también el pretil. Toda la nave a la misma altura; el portal vidriado del extremo oeste va de piso a dintel. El techo cae hacia el sur (3 % engrafado o 7 % trapezoidal), a una canaleta interna escondida detrás del pretil.

Detalle del frente norte: cenefa, brise y faja

Detalle del frente norte: cenefa, brise y faja

corte por la fachada a la plaza · escala aproximada 1:20

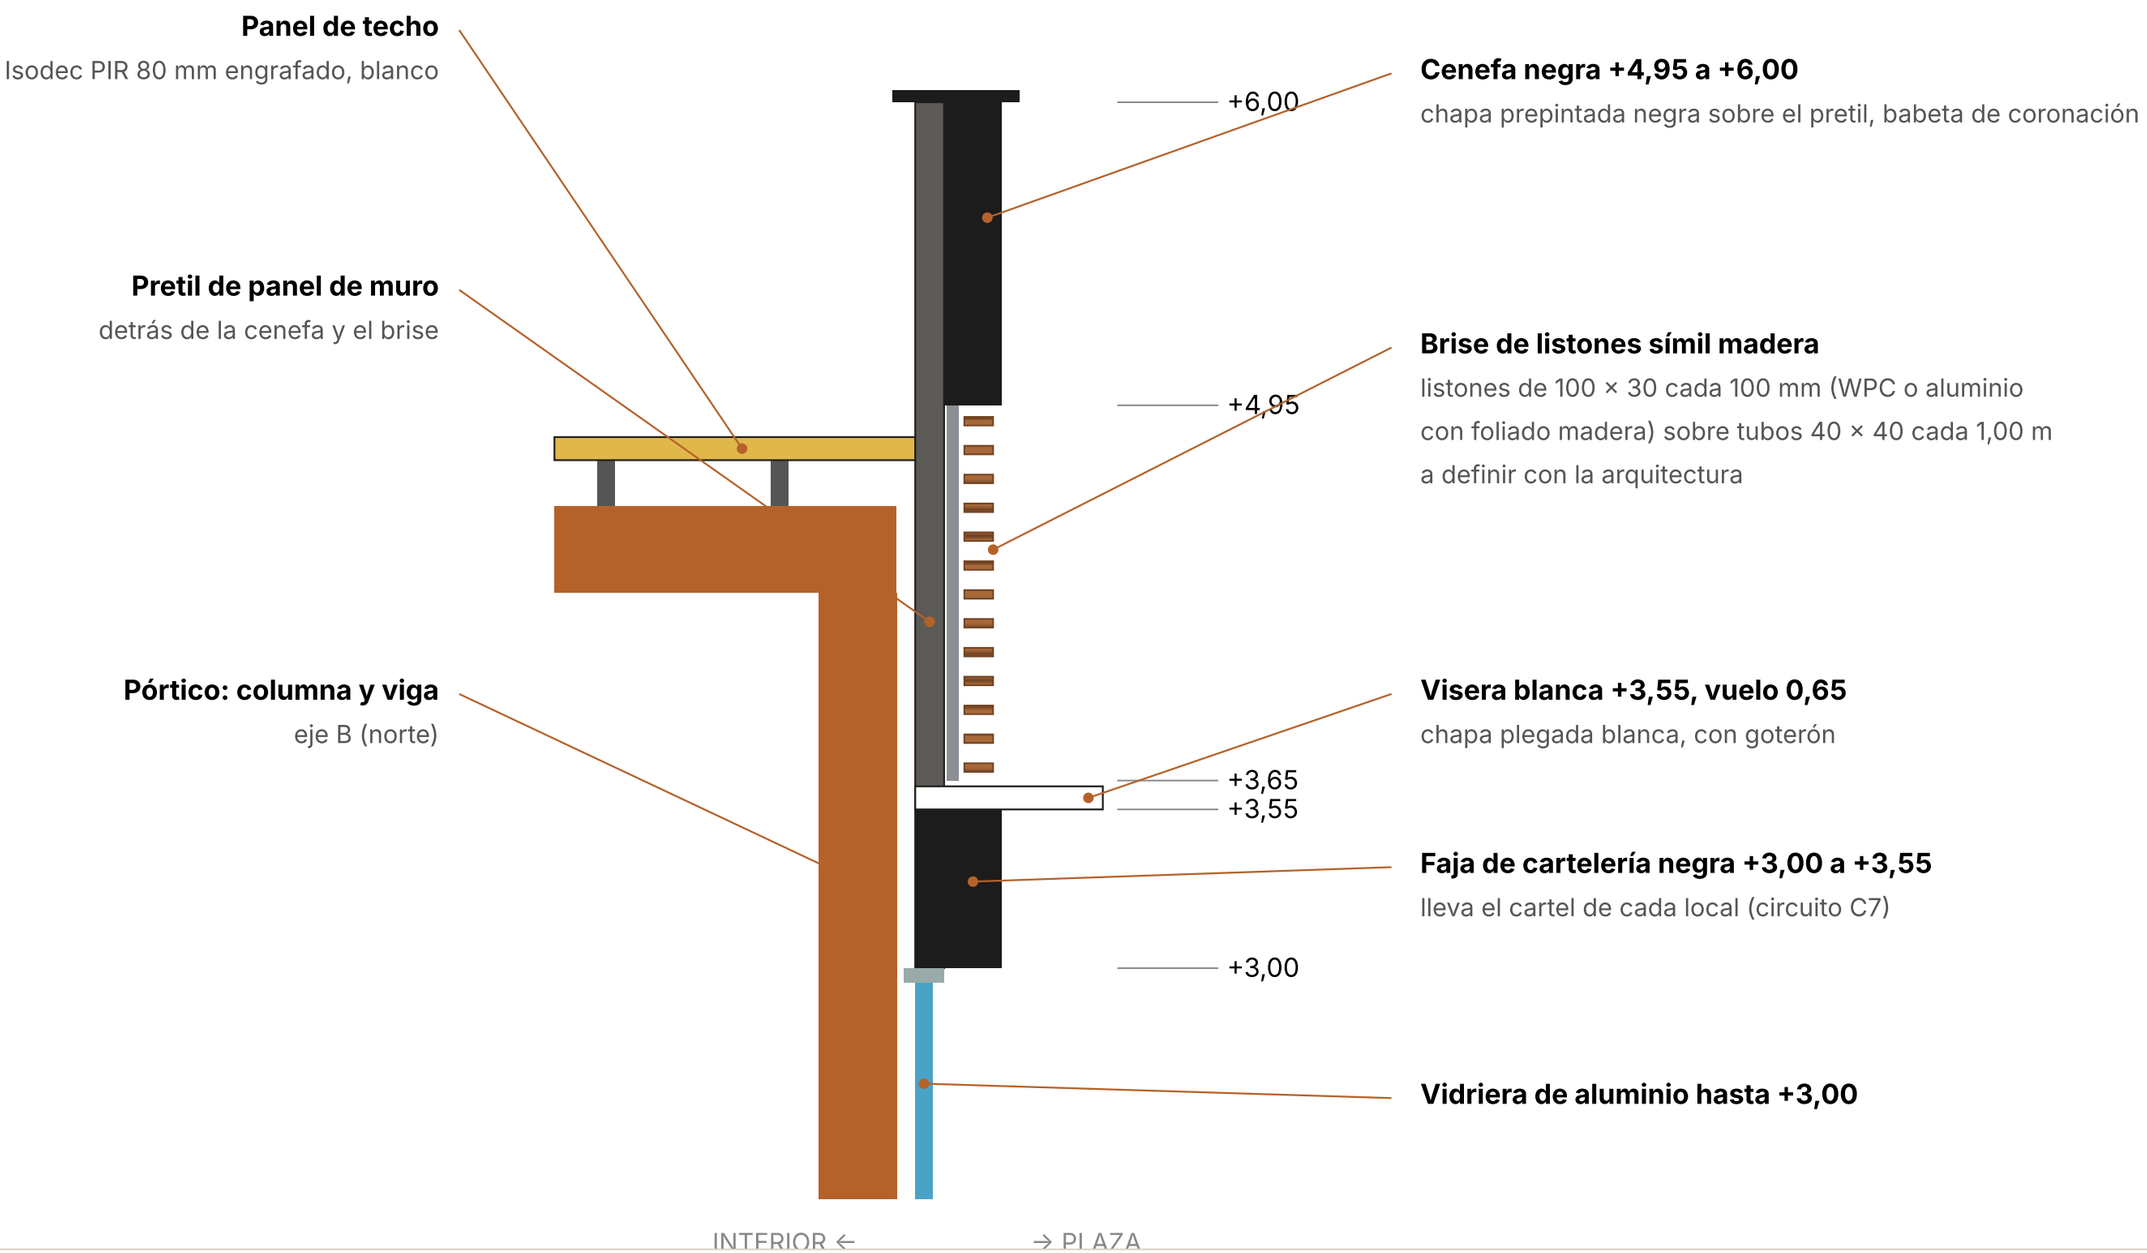


Alturas: piso terminado +0,15; vidriera hasta +3,00; faja de cartelería +3,00 a +3,50; visera blanca a +3,55; brise de +3,65 a +4,95; cenefa negra de +4,95 a +6,00, que es también el pretil. Toda la nave a la misma altura; el portal vidriado del extremo oeste va de piso a dintel. El techo cae hacia el sur (3 % engrafado o 7 % trapezoidal), a una canaleta interna escondida detrás del pretil.

Detalle del borde sur: canaleta interna, bajadas y desborde

Detalle del borde sur: canaleta interna, bajadas y desborde

corte por la fachada sur · escala aproximada 1:20

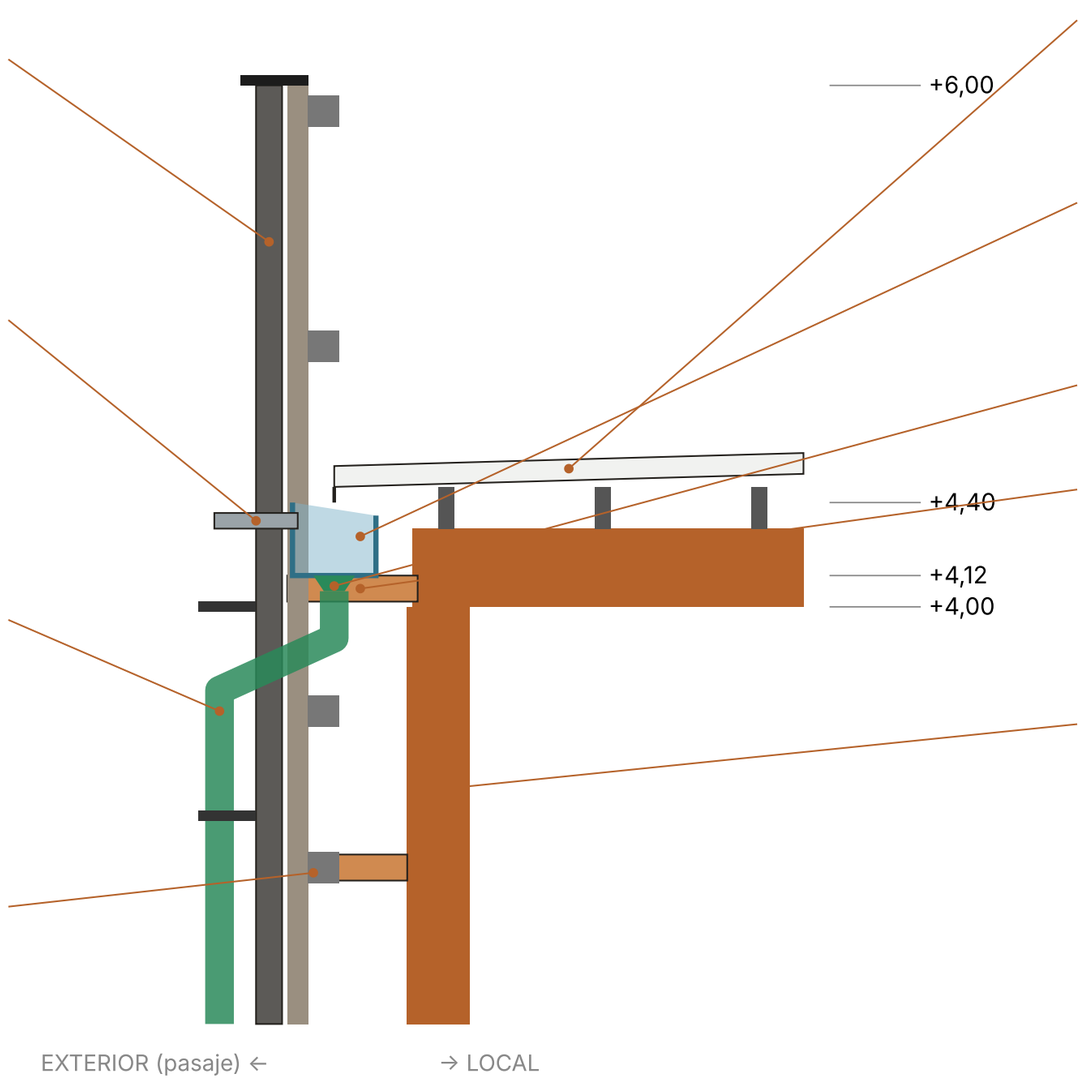

Muro sur de panel, separado 30 cm
sobre parantes 80 × 80 y largueros C120; sigue hasta +6,00 como pretil, con babeta

Gárgola de desborde, una por tramo
más baja que el borde de la canaleta: si se tapa un embudo el agua sale afuera

Bajada pluvial Ø110 por fuera
codo embutido que atraviesa el panel, grapas cada 1,5 m, del color del panel

Separador columna → parante
tubo 80 × 40 a +1,50 y +3,00

Panel de techo
Isodec PIR 80 mm engrafado, blanco, vuela 10 cm sobre la canaleta con goterón

Canaleta interna 32 × 28 cm
chapa prepintada 0,7 mm, pendiente 0,5 % hacia 3 embudos

Embudo Ø110 con canasto parahojas

Ménsula tubo 100 × 50
soldada a columna y viga carrera, vuela 0,45 m · verificar cálculo

Columna del pórtico
queda suelta por dentro del local

El muro sur se separa 30 cm de las columnas para alojar la canaleta. Las bajadas salen por un codo que atraviesa el panel y bajan por fuera hasta una boca 40 × 40; de ahí van por un colector pluvial propio a la calle, separado del cloacal (no se pueden mezclar). La platea se ensancha 0,42 m al sur para apoyar el muro. A verificar con el cálculo: ménsulas, separadores y borde de platea.

Render del anteproyecto (enviado por el cliente)

