
DESAGÜES · PLANO

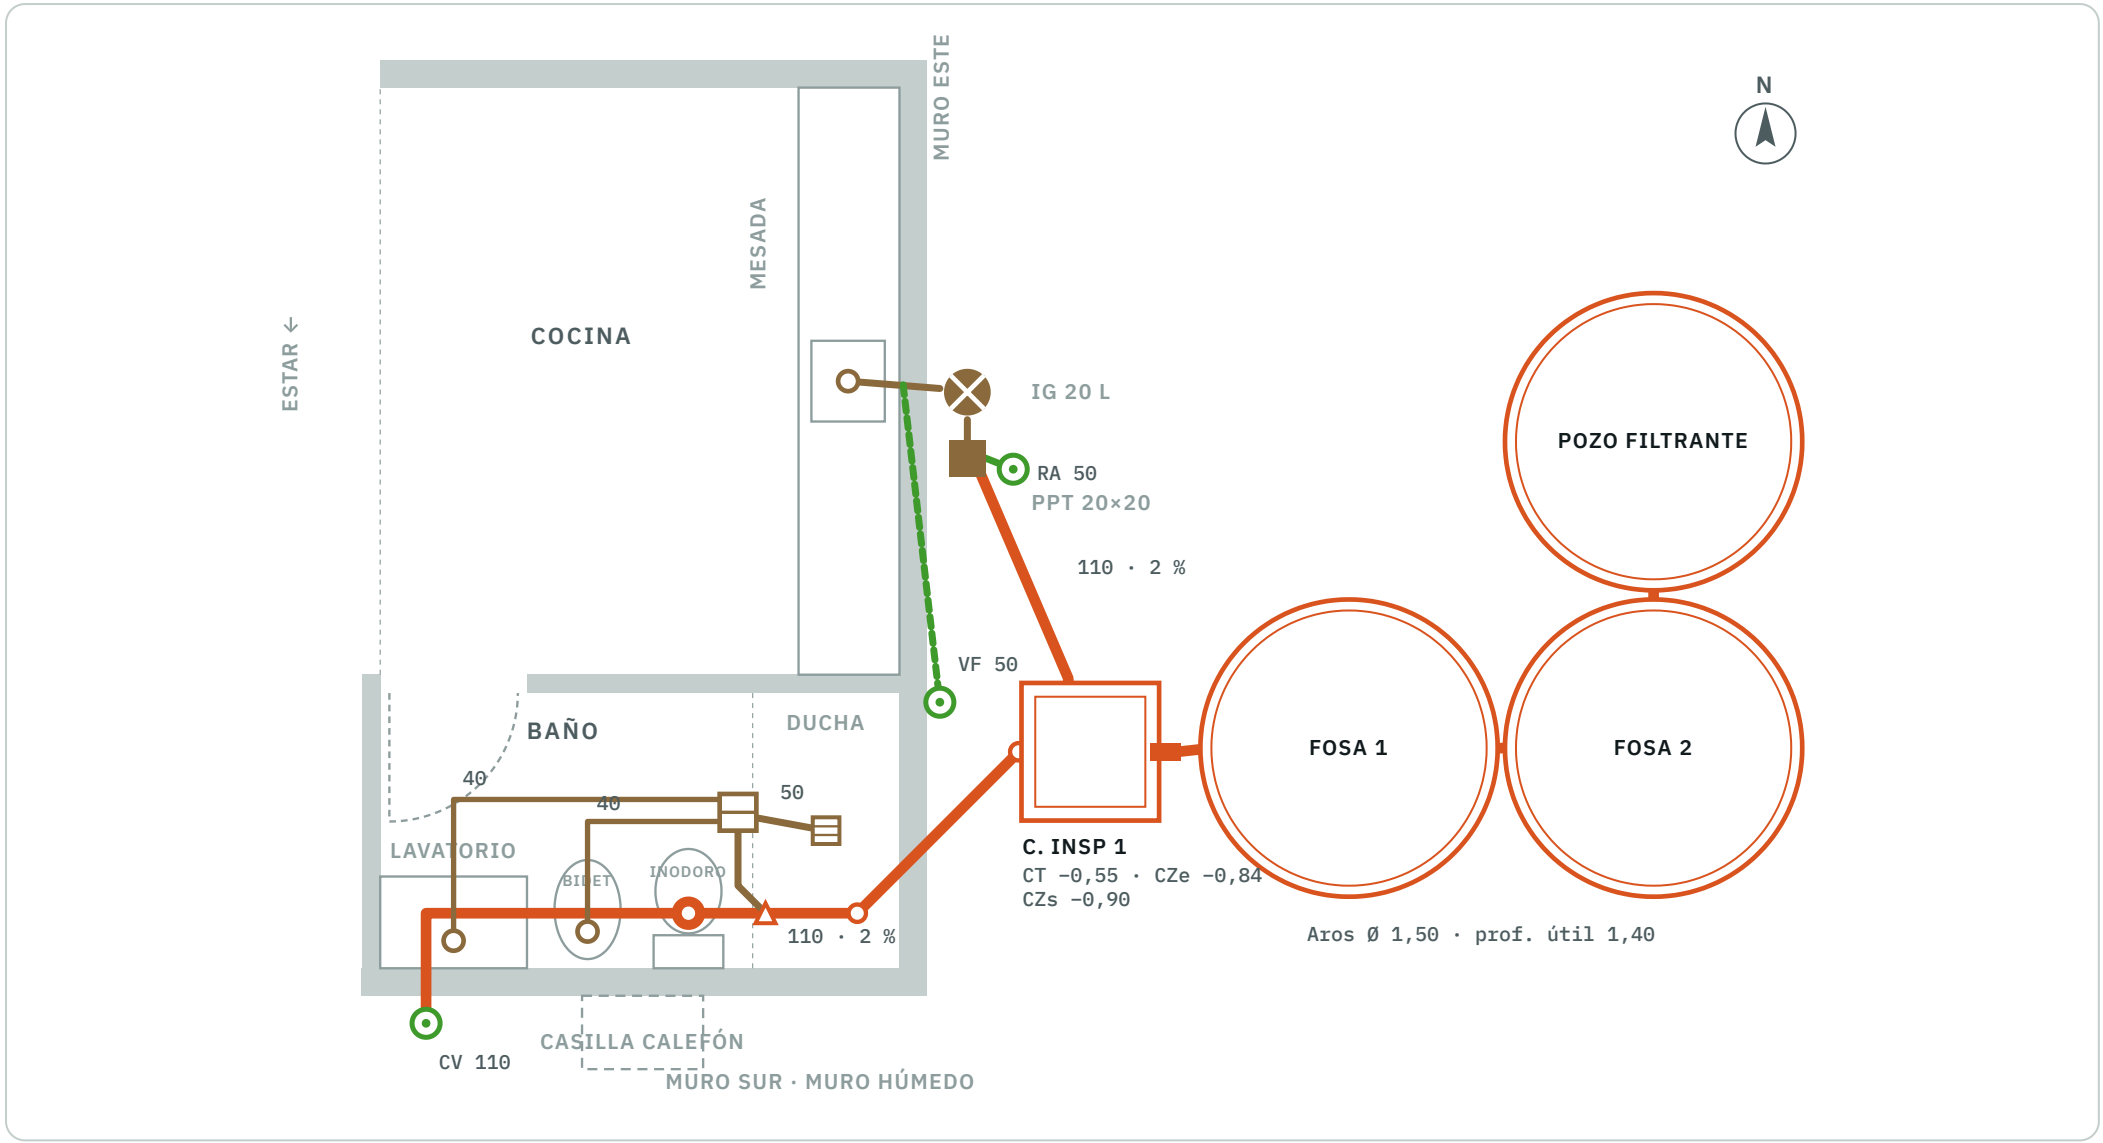

Primaria PVC 110 — Secundaria PVC 40 / 50 — Ventilación — Planta, norte arriba, como en S01

Cotas de zampeado

El piso terminado está a 0,00 y el terreno bajo la casa a −0,58 / −0,60. El colector parte de la entrada a la cámara (−0,84) con pendiente del 2 % hacia la casa, así que bajo la casa queda enterrado unos 20 cm, igual que en el corte AA.

PUNTO	DISTANCIA A LA CÁMARA	COTA	ORIGEN
Cabeza del colector (pie del CV)	4,28 m	-0,75	2 % desde CZe
Ramal del inodoro	2,25 m	-0,79	2 % desde CZe
Ramal de la caja sifonada	1,83 m	-0,80	2 % desde CZe
Paso bajo el muro este	0,80 m	-0,82	2 % desde CZe
Entrada cámara 1 (CZe)	0,00 m	-0,84	S01
Salida cámara 1 (CZs)	—	-0,90	S01
Tapa cámara 1 (CT)	—	-0,55	S01

Supuestos

DISTRIBUCIÓN DEL BAÑO
La de tus croquis: lavatorio, bidet, inodoro y ducha sobre el muro sur. S01 tiene otra distribución en el baño, pero las conexiones exteriores se toman tal cual de la lámina.

CAJA SIFONADA
Junta lavatorio, bidet y ducha y funciona como sifón de los tres, así que esos artefactos no llevan sifón propio. La salida es PVC 50 y entra al colector 110 a 45°.

INODORO
Desagüe vertical a piso con el eje a 0,30 m de la pared terminada. Revisá la ficha: hay modelos con mochila apoyada que salen a 0,20–0,25.

COCINA
Como en S01: pileta con sifón, PVC 50 al interceptor de grasa de 20 l, después a la pileta de patio tapada 20 × 20 y de ahí PVC 110 a la cámara 1. Ventilaciones VF y RA en PVC 50.

CÁMARA Y TRATAMIENTO
Cámara de inspección 1 de 0,60 × 0,60 con sifón desconector. Después van dos fosas sépticas y el pozo filtrante, todos con aros de Ø 1,50 y 1,40 m de profundidad útil (S01).

FUERA DE ALCANCE
Pluviales y la ventilación del pozo filtrante, que se hace según S01.