
AGUA FRÍA Y CALIENTE · PLANO

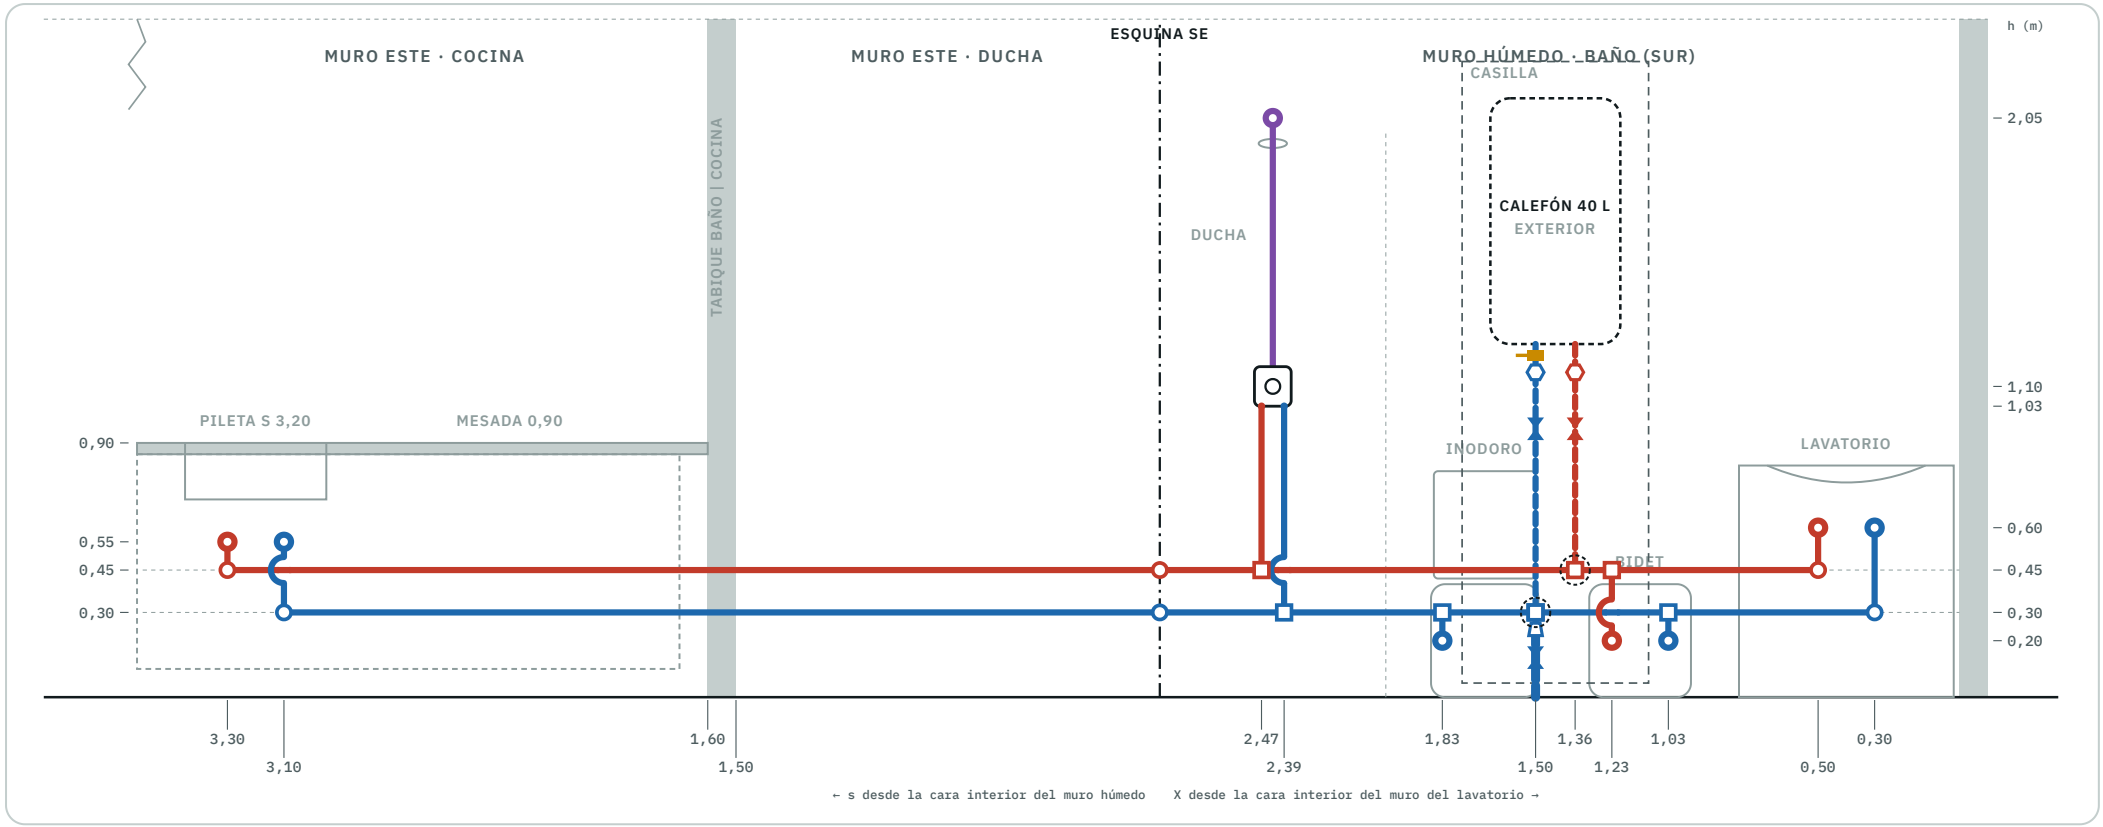

Fría · Caliente · Salida de ducha · Punteado: lado exterior, se ve espejado

Desarrollo de los dos muros vistos desde adentro. A la izquierda va el muro este (cocina y lateral de la ducha) y a la derecha el muro húmedo del baño. Se doblan en la esquina SE.

Replanteo de tomas

Muro húmedo: X desde la cara interior del muro del lavatorio. Muro este: s desde la cara interior del muro húmedo. Altura desde nivel de piso terminado (NPT). La caliente siempre a la izquierda, mirando el artefacto.

ARTEFACTO	AGUA	MURO	POSICIÓN	ALTURA	PIEZA
Lavatorio	Caliente	Húmedo	X 0,50	0,60	Codo 90° 20×½" H con base
Lavatorio	Fría	Húmedo	X 0,30	0,60	Codo 90° 20×½" H con base
Bidet	Caliente	Húmedo	X 1,23	0,20	Codo 90° 20×½" H con base
Bidet	Fría	Húmedo	X 1,03	0,20	Codo 90° 20×½" H con base
Inodoro (mochila)	Fría	Húmedo	X 1,83	0,20	Codo 90° 20×½" H con base
Ducha · monocomando	Fría + caliente	Húmedo	X 2,43	1,10	Cuerpo embutido; entradas a 1,03 (C X 2,47 · F X 2,39), 3 conectores 20×½" M
Ducha · salida brazo	Mezcla	Húmedo	X 2,43	2,05	Codo 90° 20×½" H con base
Pileta de cocina	Caliente	Este	s 3,30	0,55	Codo 90° 20×½" H con base
Pileta de cocina	Fría	Este	s 3,10	0,55	Codo 90° 20×½" H con base

Supuestos

CALEFÓN
40 l (S01), en el muro exterior centrado detrás del bidet y el inodoro (eje X 1,43), dentro de una casilla. La entrada fría a la derecha y la salida caliente a la izquierda mirándolo de frente, separadas 14 cm.

INODORO
Con mochila apoyada: una toma fría a 0,20 m, 15 cm a la izquierda del eje.

DUCHA
Monocomando embutido. Cuerpo a 1,10 m con entradas abajo (caliente X 2,47 · fría X 2,39) y salida de brazo a 2,05 m.

COCINA
Pileta sobre el muro este, a unos 3,20 m de la cara interior del muro húmedo, medido a escala en S01. Hay que medirlo en obra. Tomas a 0,55 m, 20 cm entre sí, para mezcladora con flexibles.

RECORRIDO A LA COCINA
Las horizontales siguen desde la ducha, doblan en la esquina SE y van por el muro este, pasando el encuentro con el tabique, hasta la pileta. Fría a 0,30 y caliente a 0,45.

CAÑO
PPR PN20. 20 mm dentro de la casa y 25 mm en la llegada desde el medidor de OSE (S01: "PPT diam. 25mm").